

RESIDENTIAL

JOB # 25243 Premier - Lot 4
STAIN-1 "COFFEE BEAN" VERTICAL

JOB NOTES

Work Order Specs.	
Cab Exterior	SELECT ALDER VENEER
Cab Interior	PREFINISHED MAPLE PLY
Doors	5-Piece 2 1/4" Shaker Sq Flat Panel, E4 P39
Drawer Front	5-Piece 2 1/4" Shaker Sq Flat Panel, E4 P39
Drawer / Rollout Box	Birch Ply Dovetail
Finish Specs.	
Stain	COFFEE BEAN
Finish	Conversion Varnish
Sheen	Dull
Touchup Kit	COFFEE BEAN
Fastcaps	COFFEE BEAN

Work Order Hardware	
Hinge	Blum 110 Int-Soft Close
Drawer Guides	Full Extension Soft Close Undermount
Rollout Guides	Full Extension Sidemount
(QTY) Door and Drawer PULL-1	PROVIDED BY OTHERS
Shelf Clips	5MM Nickel Pin
(QTY) Floating Shelf Bracket	
(1) Trash Pullout	4WCTM-18BBSCDM2
(2) PRODUCE STORAGE	4SSB-18-MP
(1) Lazy Susan	LD-4NW-472-28-1
(QTY) Tray Dividers	
(QTY) Closet Rod	

MOLDINGS			
Type	Size	Material	Qty Needed
Toe skin	1/4" x 4" x 96"	1/4 SELECT ALDER Veneer	LF
Base Shoe	7/8" x 1/2" w/ 1/4" Chamfer Edge	SELECT ALDER	LF
Filllers	2 1/2" x 2 1/2" "L" Shaped	SELECT ALDER	LF
Light Rail	Flat 13/16" x 2 3/4" w 1/8" Radius Edges	SELECT ALDER	LF
Crown Nailer	Flat 2 1/4"	SELECT ALDER	LF
Crown Molding	CR- 301 - 3 1/4"	ALDER	LF
Base			

Work Order EdgeBand Schedule						
ID	Thickness	Manufacturer	#	Description	Where Used	Notes
D	.018	ESI	CUSTOM	SELECT ALDER VENEER	Applied End Panels / Door & Drawer Fronts	
E	.018	ESI		STN 1	Cabinet Body Parts	
I	.018	ESI		STN 1	Adjustable Shelves	
V	.018	ESI		STN 1	Bottom of Upper F.E.	
U	.018	ESI		STN 1	Bottom of Upper UN-F.E.	
B	.018	STOCK	STOCK	PF MAPLE	Drawer Box Sides	
C	.018	STOCK	STOCK	PF MAPLE	Drawer Box Front and Backs	
X					Misc Parts	

250 W Anton Ave.
Coeur d' Alene
Idaho 83815
(208) 772-2377



Premier - Lot 4

COVER SHEET STN

Job #
25243
WO #
0000
Project MGR

Engineer

Date
12/05/25

1 of 19

RESIDENTIAL

JOB # 25243 Premier - Lot 4
MEL-1 AGT 734 WHITE SOFT TOUCH

JOB NOTES

LOCATION: LOWER BAR



Work Order Specs.	
Cab Exterior	WHITE SOFT TOUCH
Cab Interior	HARDROCK MAPLE MEL
Doors	SLAB
Drawer Front	SLAB
Applied End Panels	NONE
Drawer / Rollout Box	PRINT MEL.
Finish Sched.	
Touchup Kit	PENS TO MATCH
Fastcaps	TO MATCH

Work Order Hardware	
Hinge	Blum 110 Int-Soft Close
Drawer Guides	FULL EXTENSION SOFT CLOSE UNDERMOUNT
Rollout Guides	FULL EXTENSION SIDEMOUNT
(QTY) Door and Drawer Pulls	
Shelf Clips	STANDARD
Trash Pullout	
PRODUCE BASKETS	(2) 4SSB-18-MPMB
Lazy Susan	
Tray Dividers	
Closet Rod	

MOLDINGS			
Type	Size	Material	Qty Needed
Toe skin	1/4" x 4" x 96"	MEL-1	LF
Base Shoe	7/8" x 1/2" w/ 1/4" Chamfer Edge		LF
Scribe Molding	7/8" x 14" w/ 1/16" Radius Edge		LF
Fillers	2 1/2" x 2 1/2" "L" Shaped	MEL-1	LF
Light Rail	Flat 13/16" x 2 3/4" w 1/8" Radius Edges		LF
Crown Molding	Flat 2 1/4"		LF
Base	CR- 401 - 4 1/4"		LF

Work Order EdgeBand Schedule						
ID	Thickness	Manufacturer	#	Description	Where Used	Notes
D	1MM	N/A	0000		Applied End Panels / Door & Drawer Fronts	
E	1MM	ESI	ESI-4905		Cabinet Body Parts	
I	.018	STOCK	STOCK	HARDROCK MAPLE MEL	Adjustable Shelves	
V	.018	ESI	ESI-4905		Bottom of Upper F.E.	
U	.018	STOCK	STOCK		Bottom of Upper UN-F.E.	
B	.018	STOCK	STOCK	PF MAPLE	Drawer Box Sides	
C	.018	STOCK	STOCK	PF MAPLE	Drawer Box Front and Backs	
X	1MM				Open Adjustable Shelves	

250 W Anton Ave.
Coeur d' Alene
Idaho 83815
(208) 772-2377



Premier - Lot 4

COVER SHEET MEL

Job #
25243
WO #
0000
Project MGR

Engineer

Date
12/05/25

RESIDENTIAL


JOB # 25243 Premier - Lot 4

JOB NOTES

APPLIED PANELS TO STOP SHORT OF THE FLOOR UNLESS OTHERWISE NOTED

INSTALLER NOTES

DESIGN NOTES

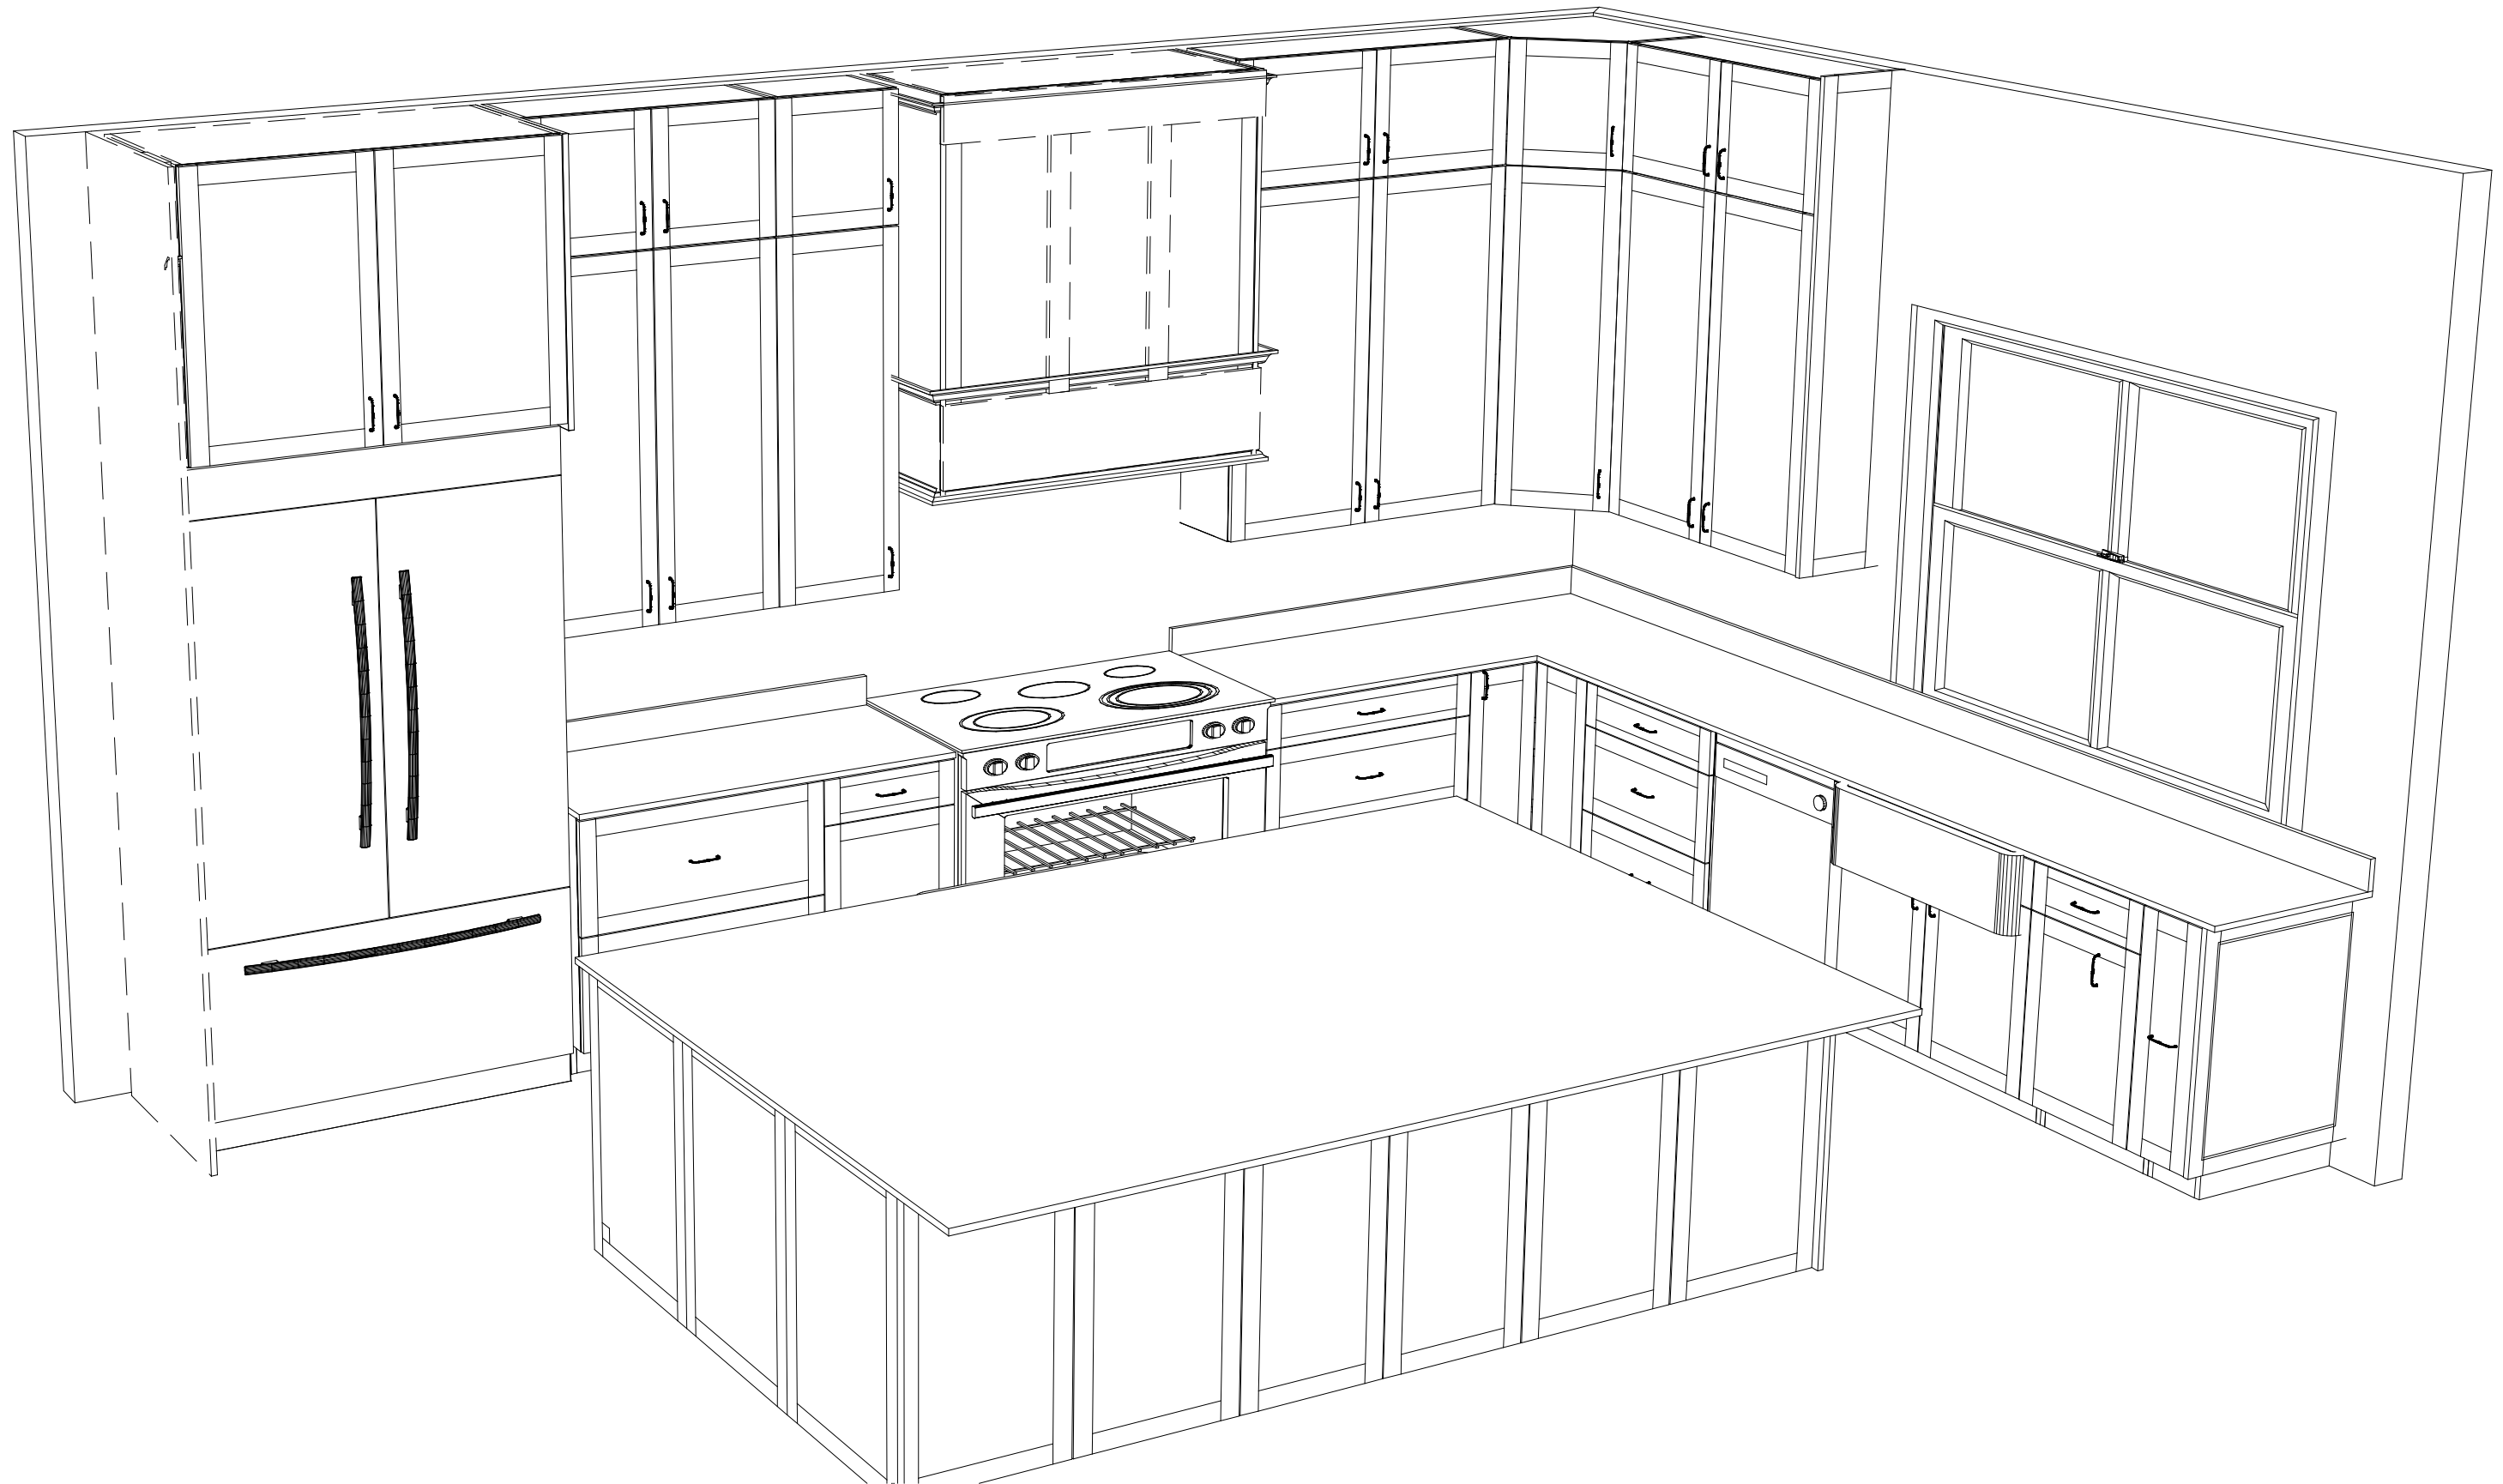

250 W Anton Ave.
Coeur d' Alene
Idaho 83815
(208) 772-2377

ADVANCED
CABINETS



Premier - Lot 4

KITCHEN 3D

Job #
25243


WO #
0000

Project MGR


Engineer

Date
12/05/25

4 of 19

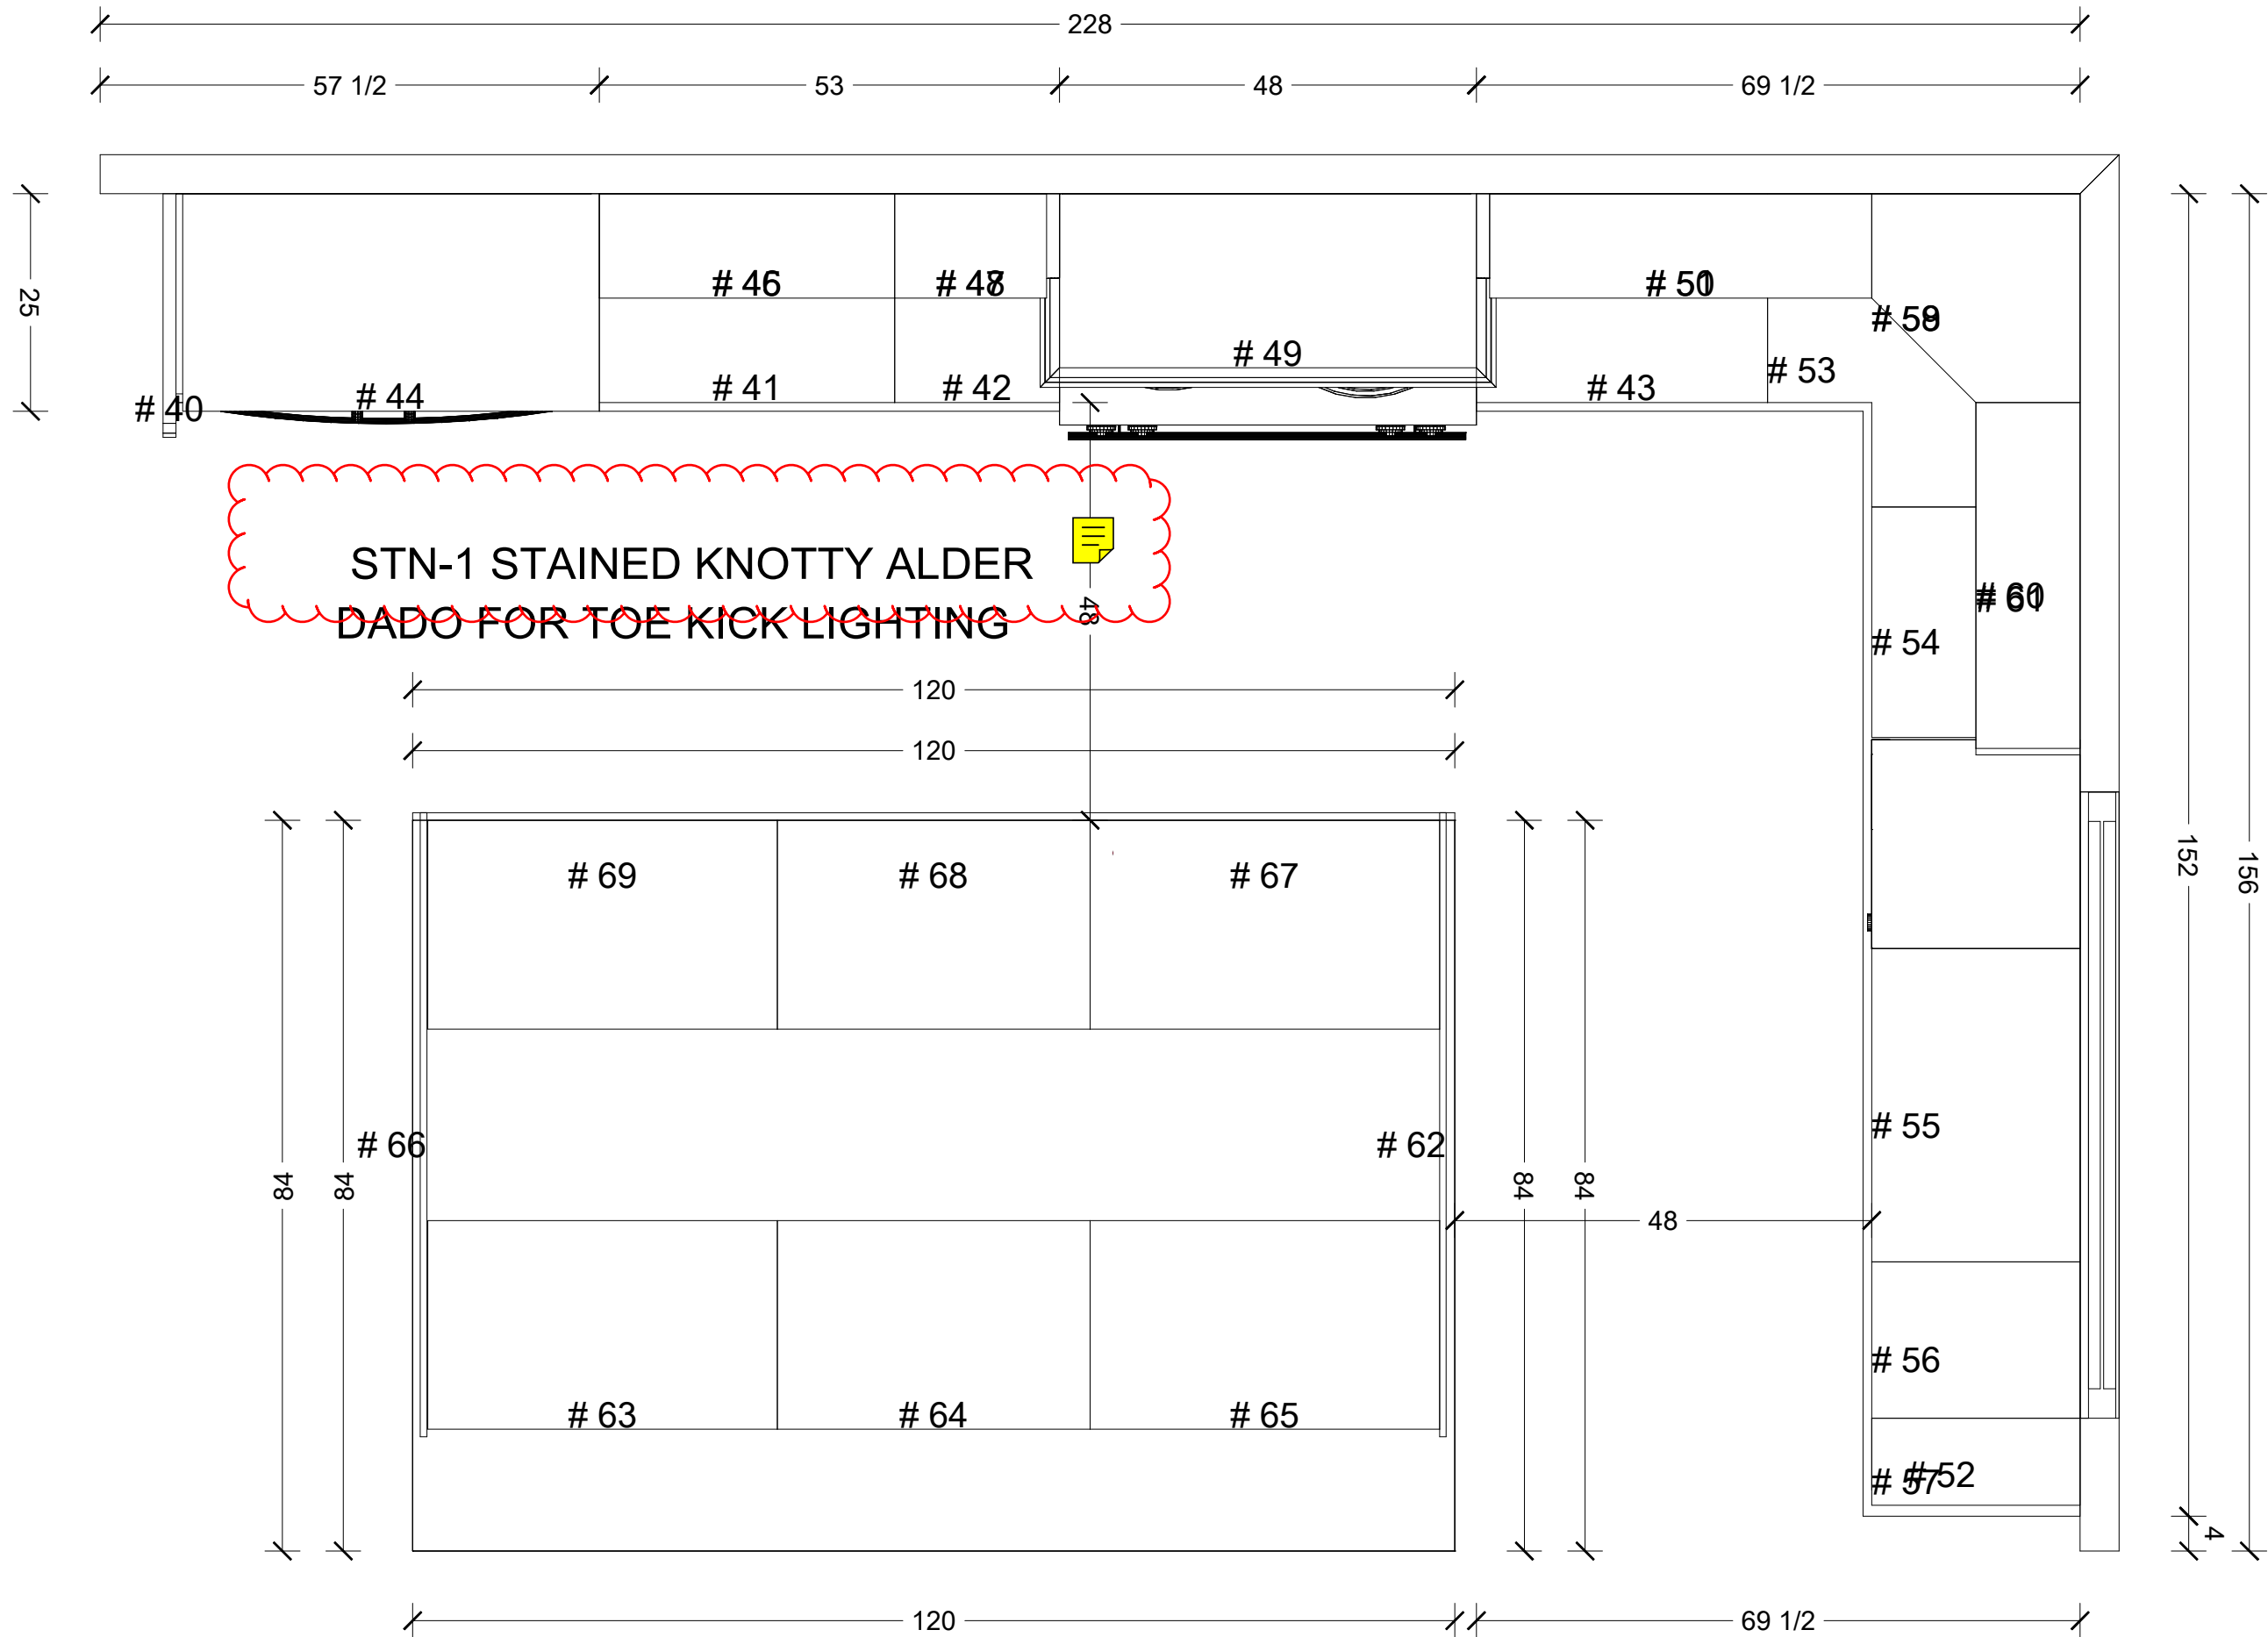

9 1/2 48 34 17 1/2 1 1/2 48 1 1/2 44 24

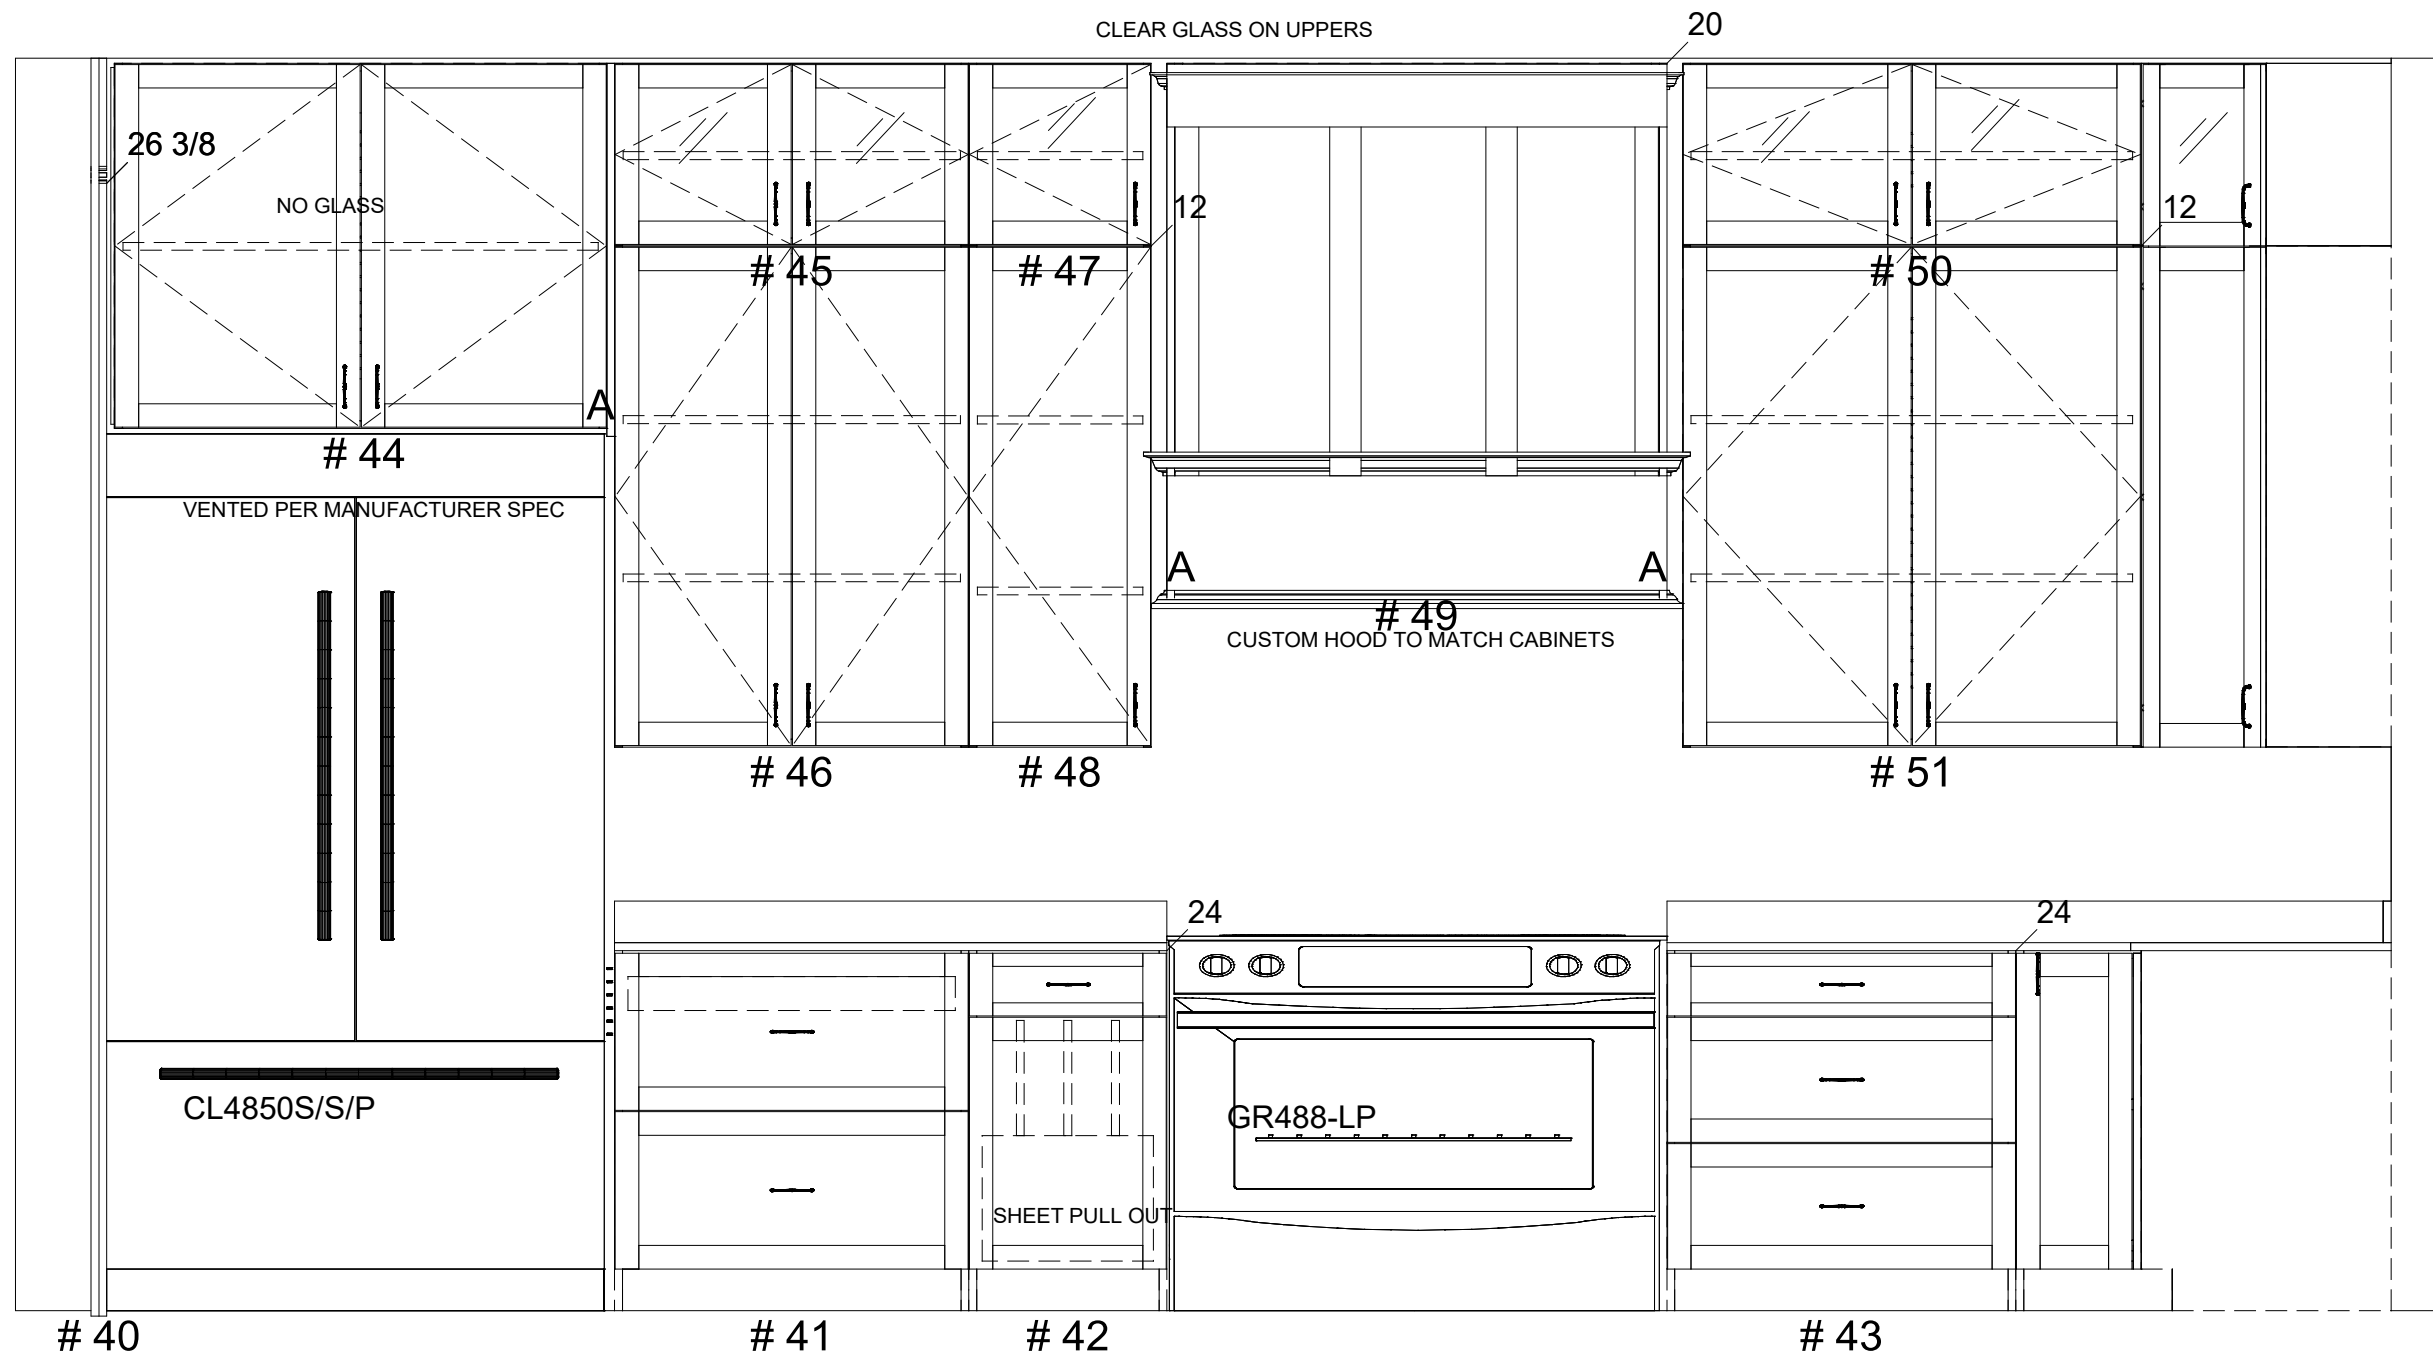

7 1/4 48 3/4 34 19 48 33 1/2 36 1 1/2

3/4 80 3/4 1/2 6 11 1/2 17 1/2 15 15 19 1/2 34 1/2 34 1/2

1/2 6 11 1/2 17 1/2 15 15 19 1/2 34 1/2 34 1/2 3/4 80 3/4 1/2


250 W Anton Ave.
Coeur d' Alene
Idaho 83815
(208) 772-2377



ADVANCED
CABINETS



Premier - Lot 4
KITCHEN WALL 2

Job #
25243
WO #
0000
Project MGR
Engineer
Date
12/05/25
6 of 19

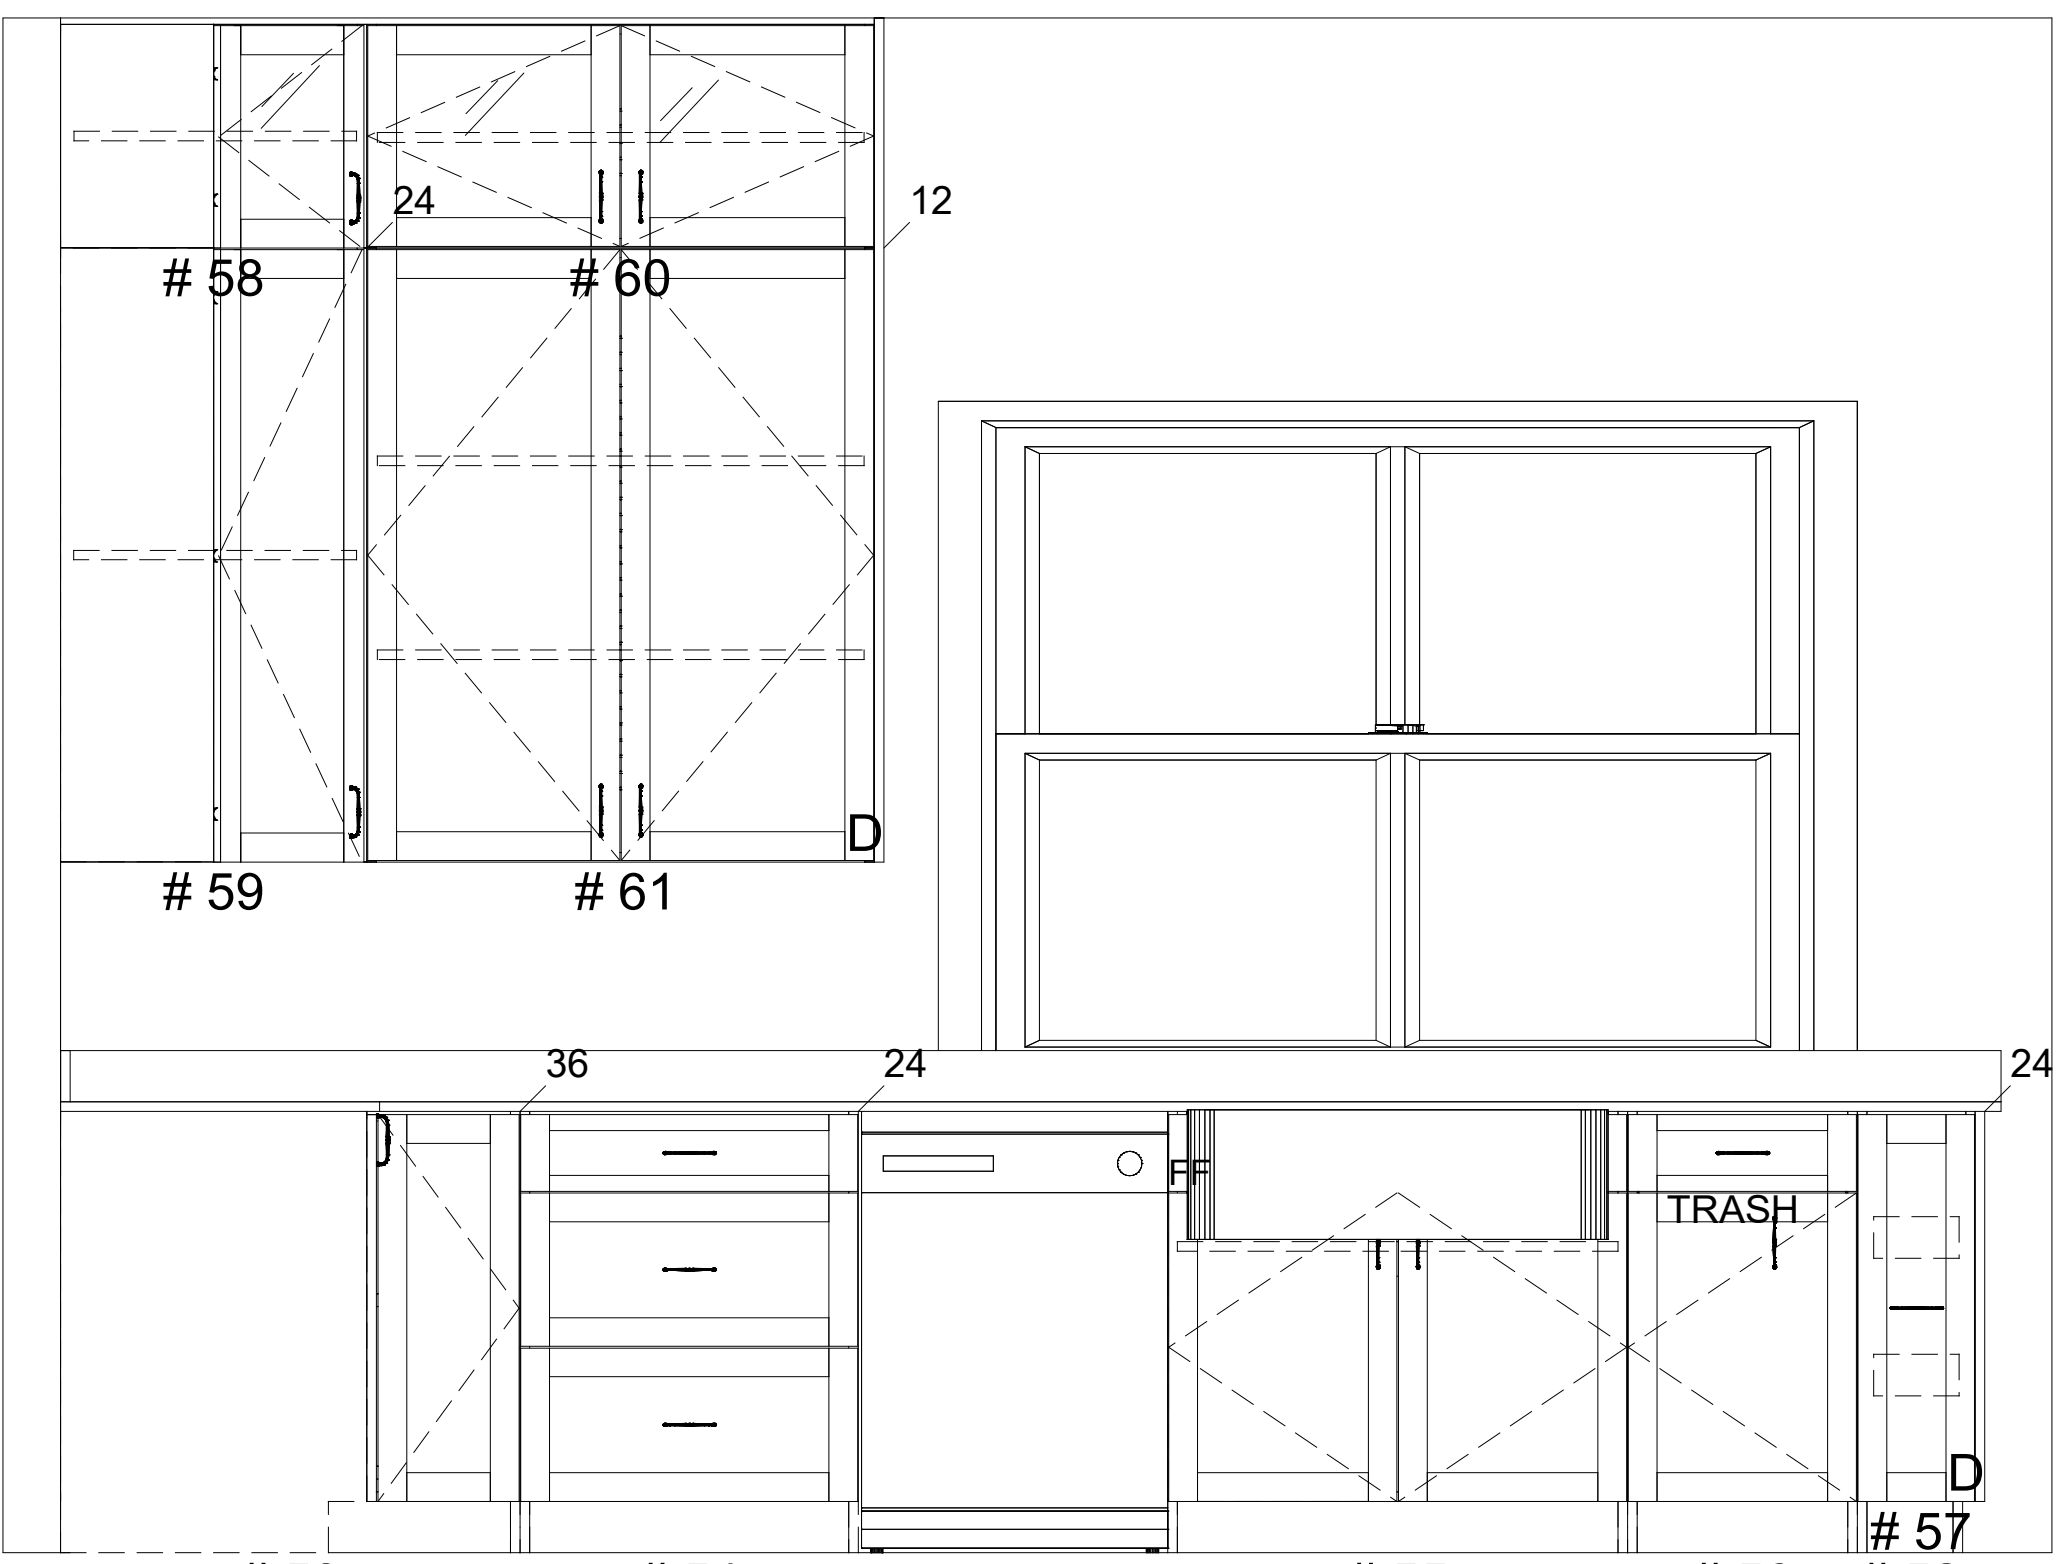

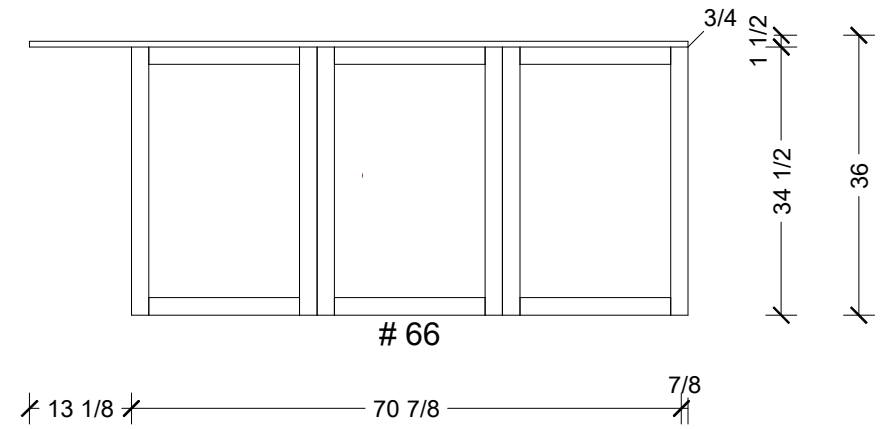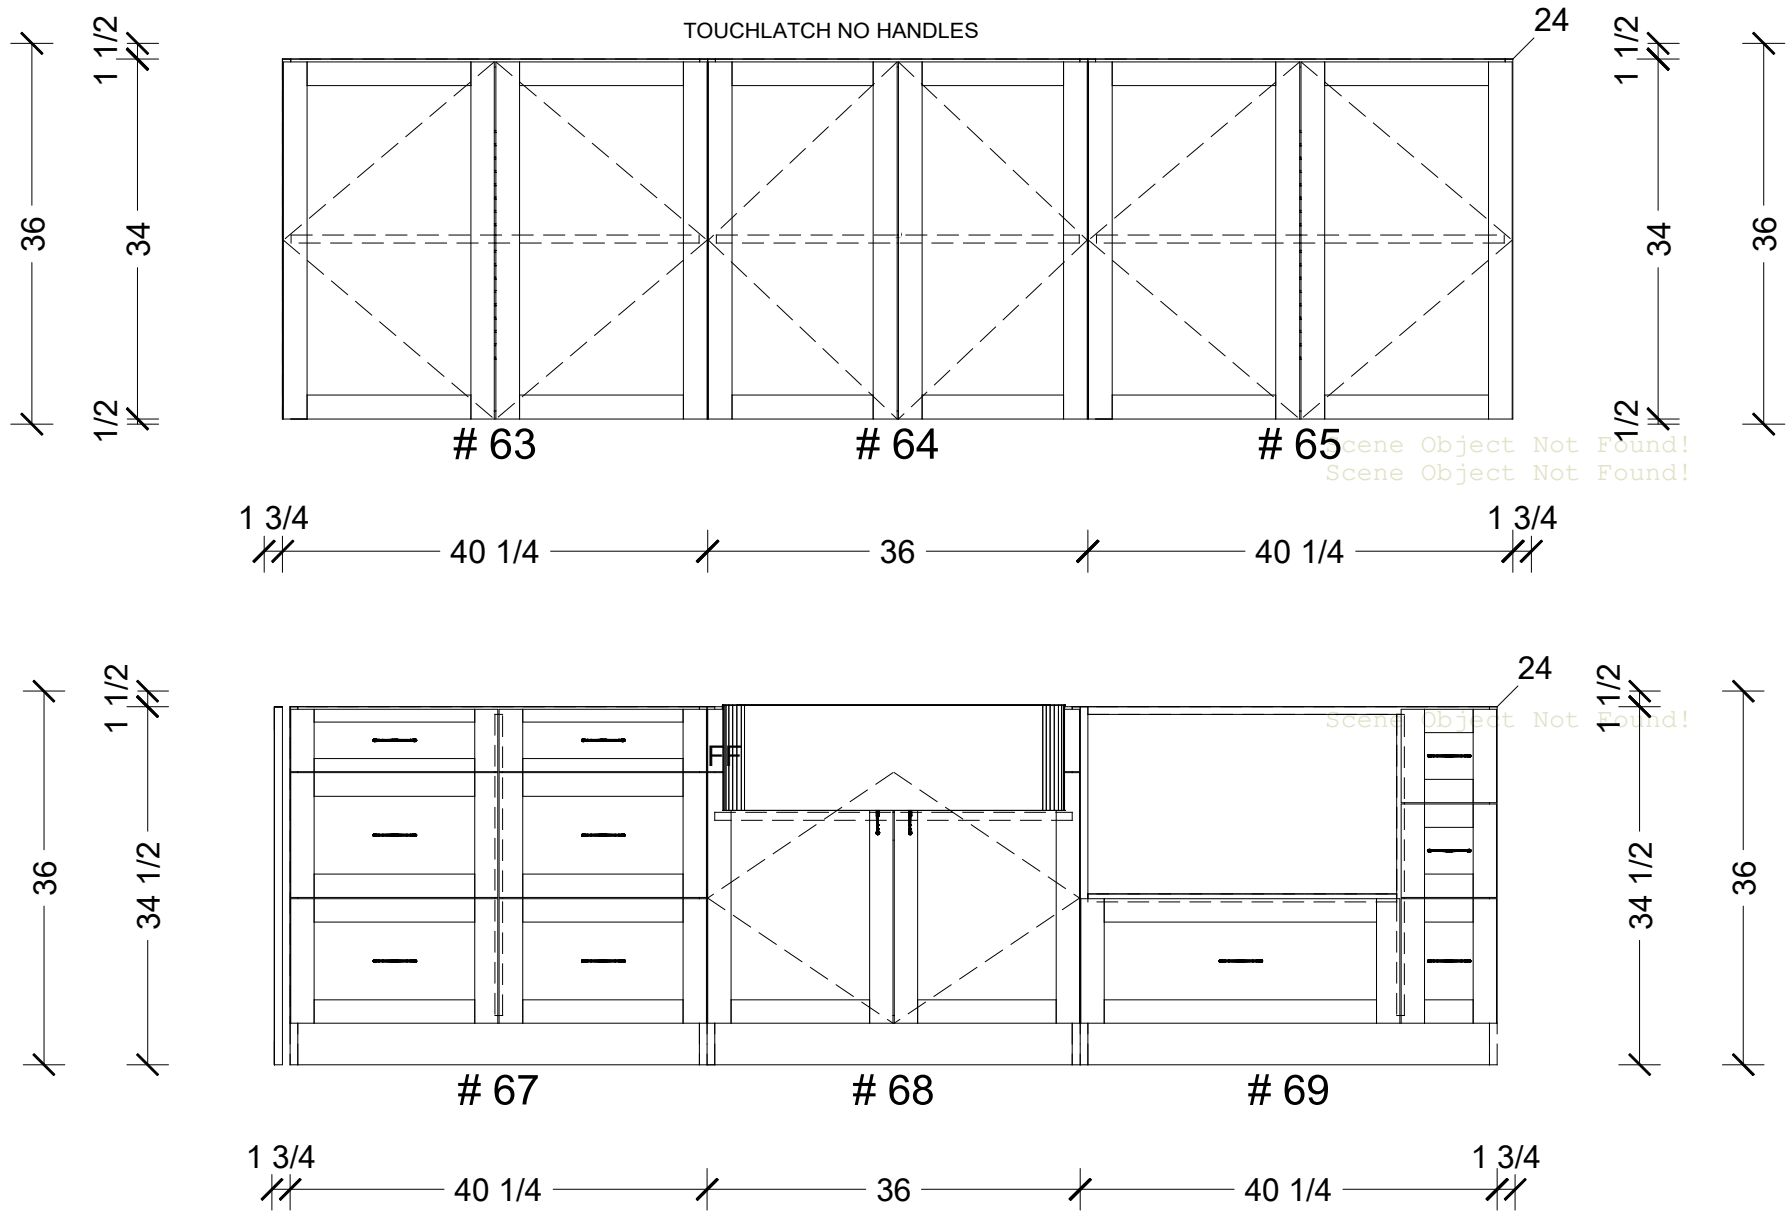



Scene Object Not Found!
Scene Object Not Found!

250 W Anton Ave.
Coeur d' Alene
Idaho 83815
(208) 772-2377




Premier - Lot 4
ISLAND ELEVATIONS

Job #
25243
WO #
0000
Project MGR
Engineer
Date
12/05/25
8 of 19

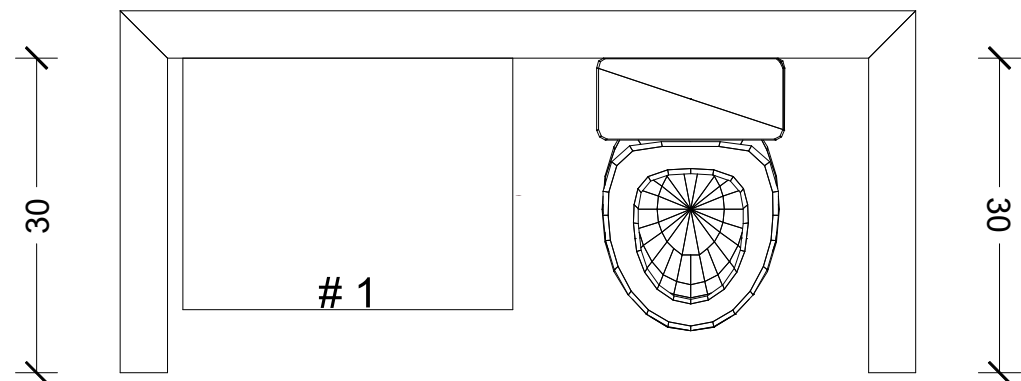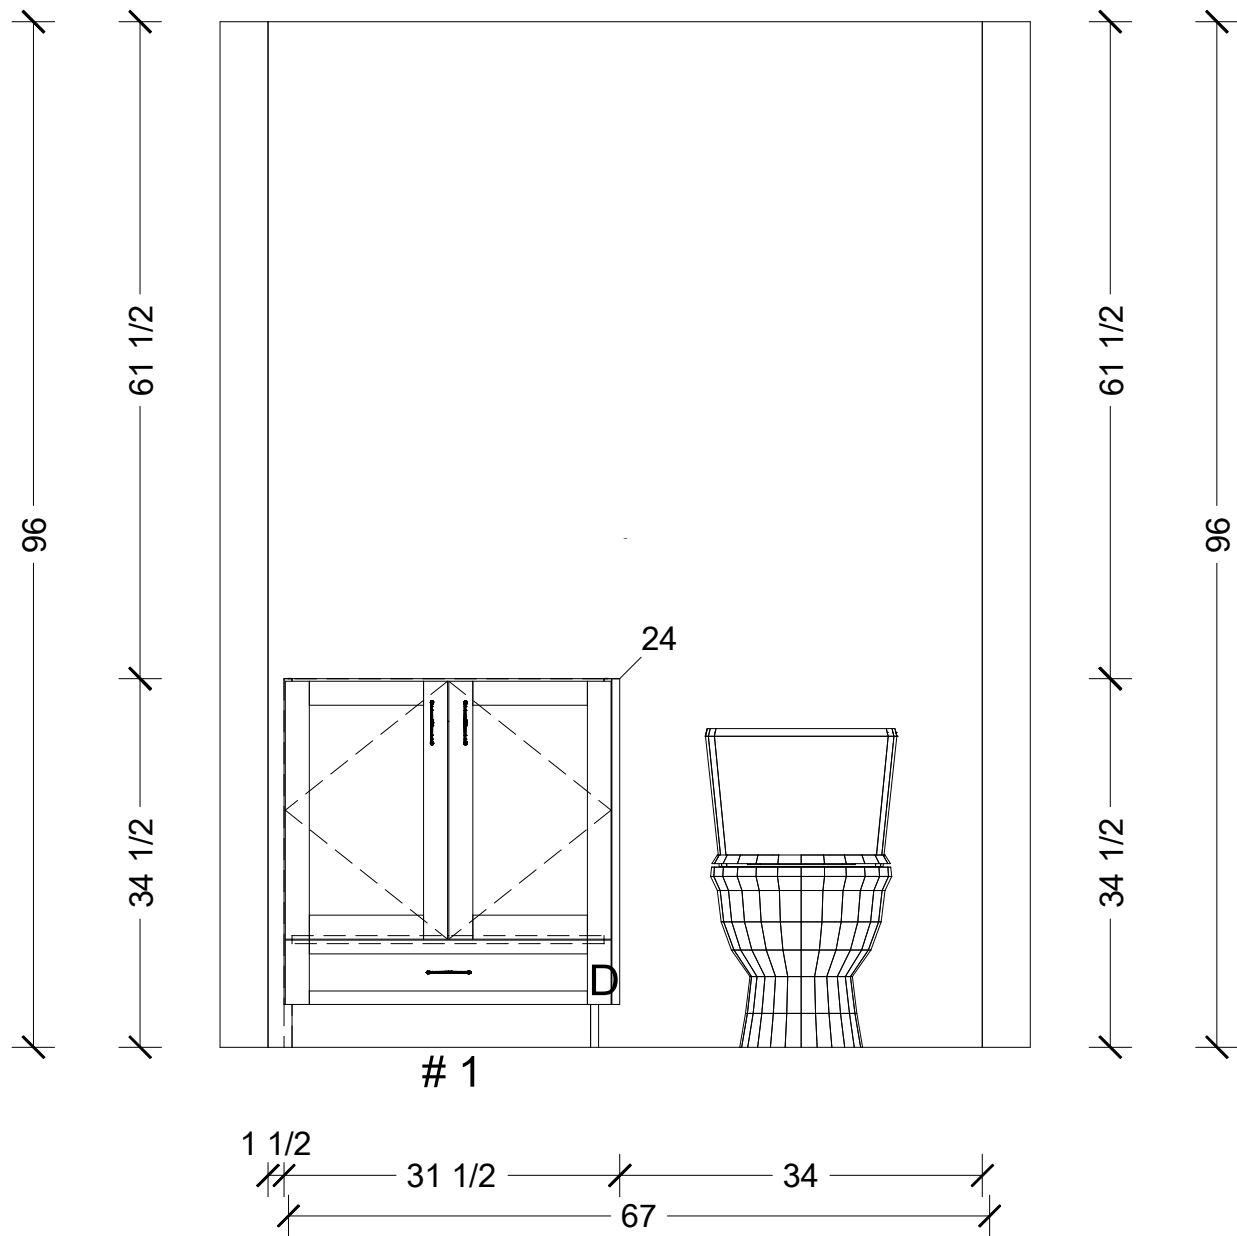

STN-1 STAINED KNOTTY ALDER

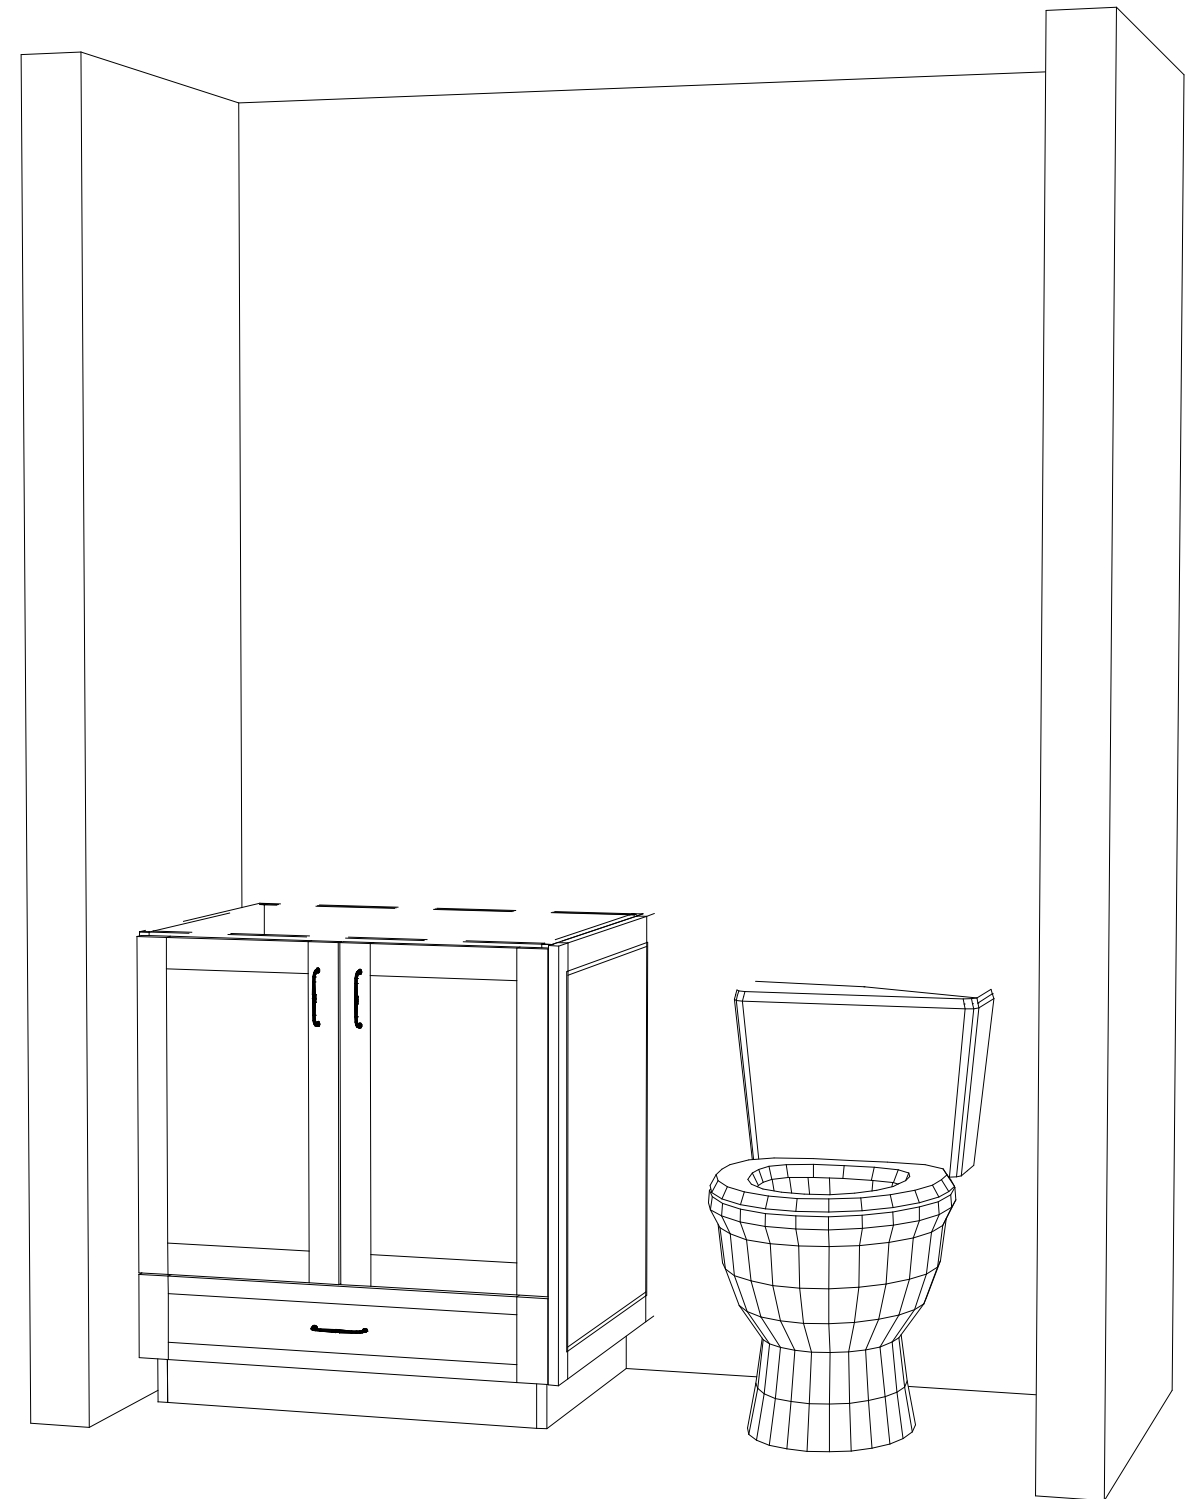

250 W Anton Ave.
Coeur d' Alene
Idaho 83815
(208) 772-2377



Premier - Lot 4

POWDER

Job #
25243




WO #
0000

Project MGR




Engineer


Date
12/05/25

9 of 19

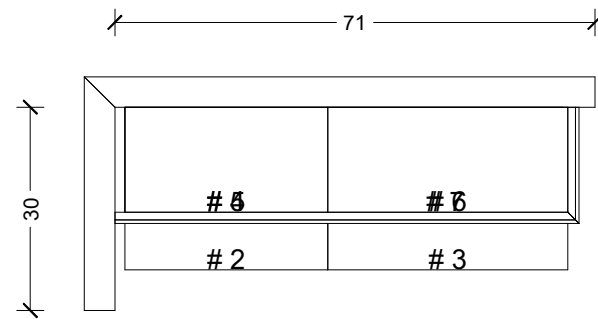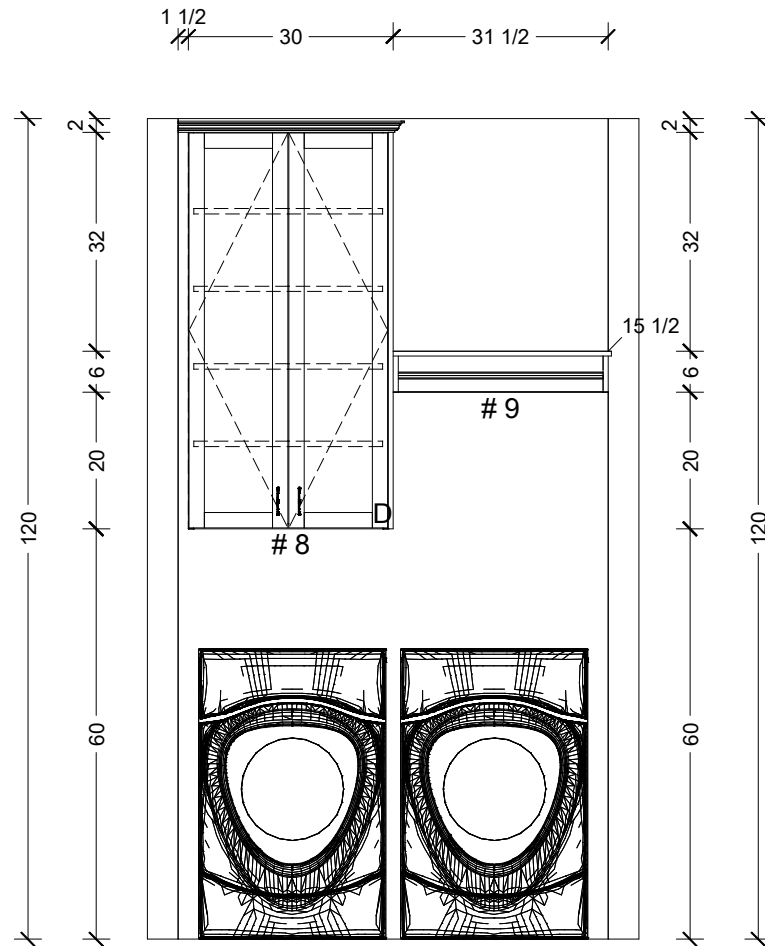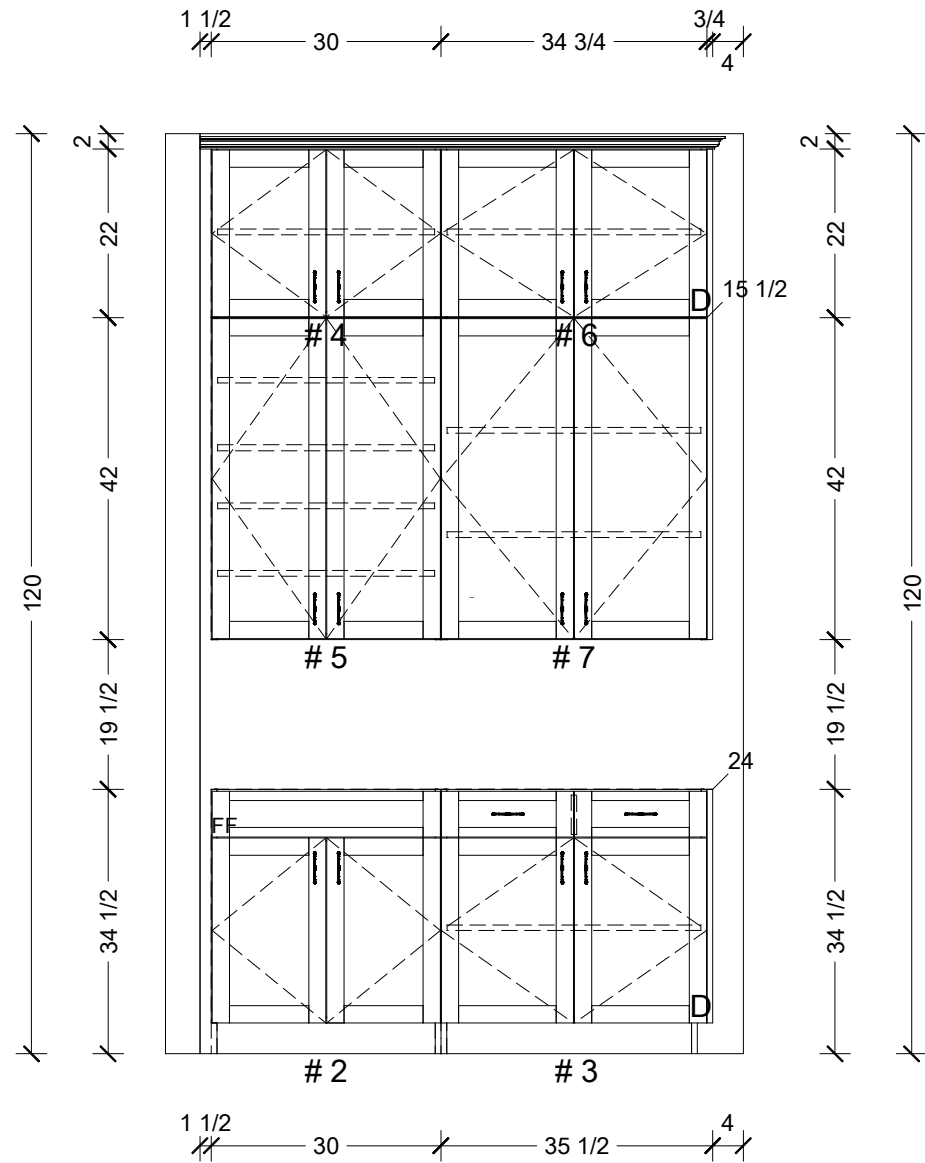


STN-1 STAINED KNOTTY ALDER

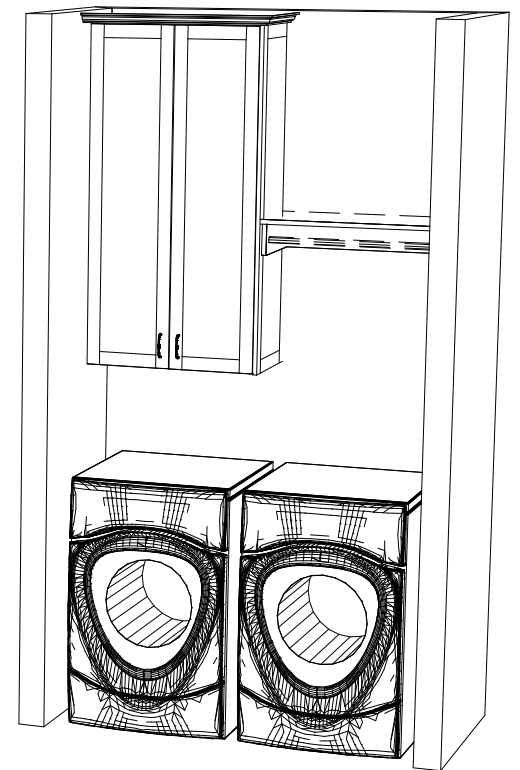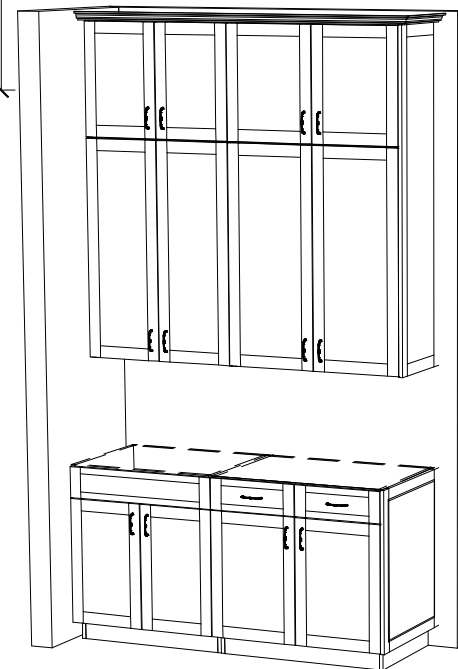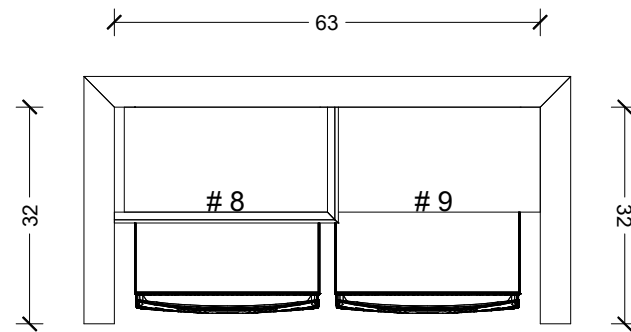

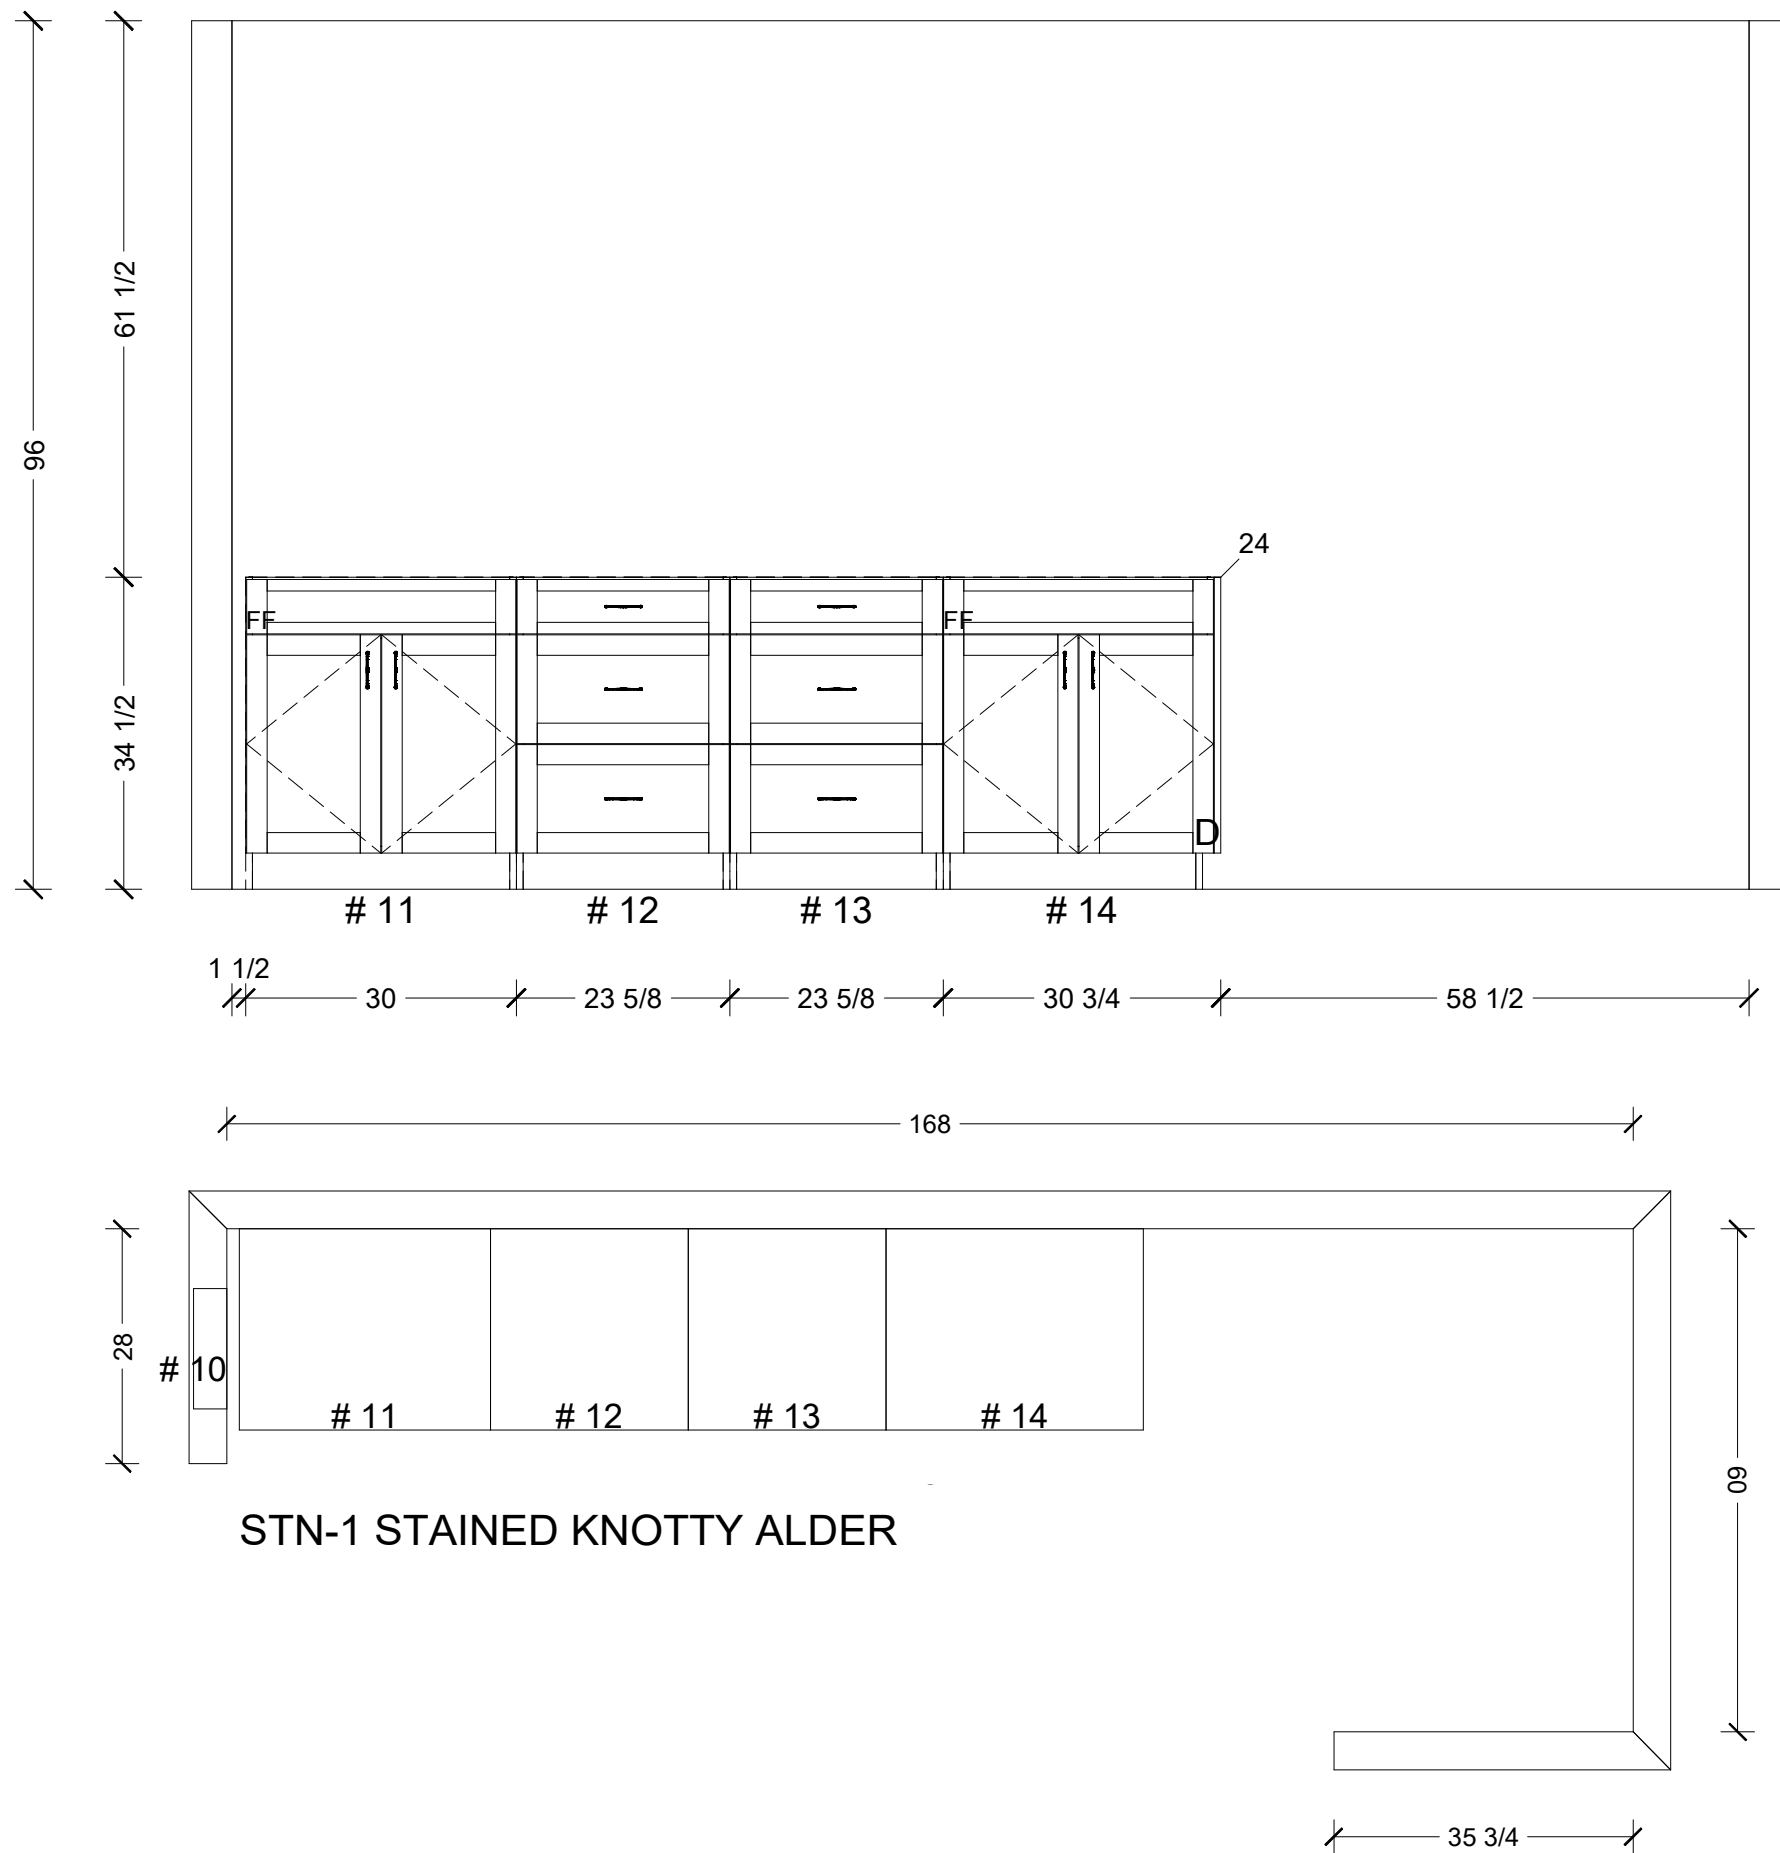

STN-1 STAINED KNOTTY ALDER

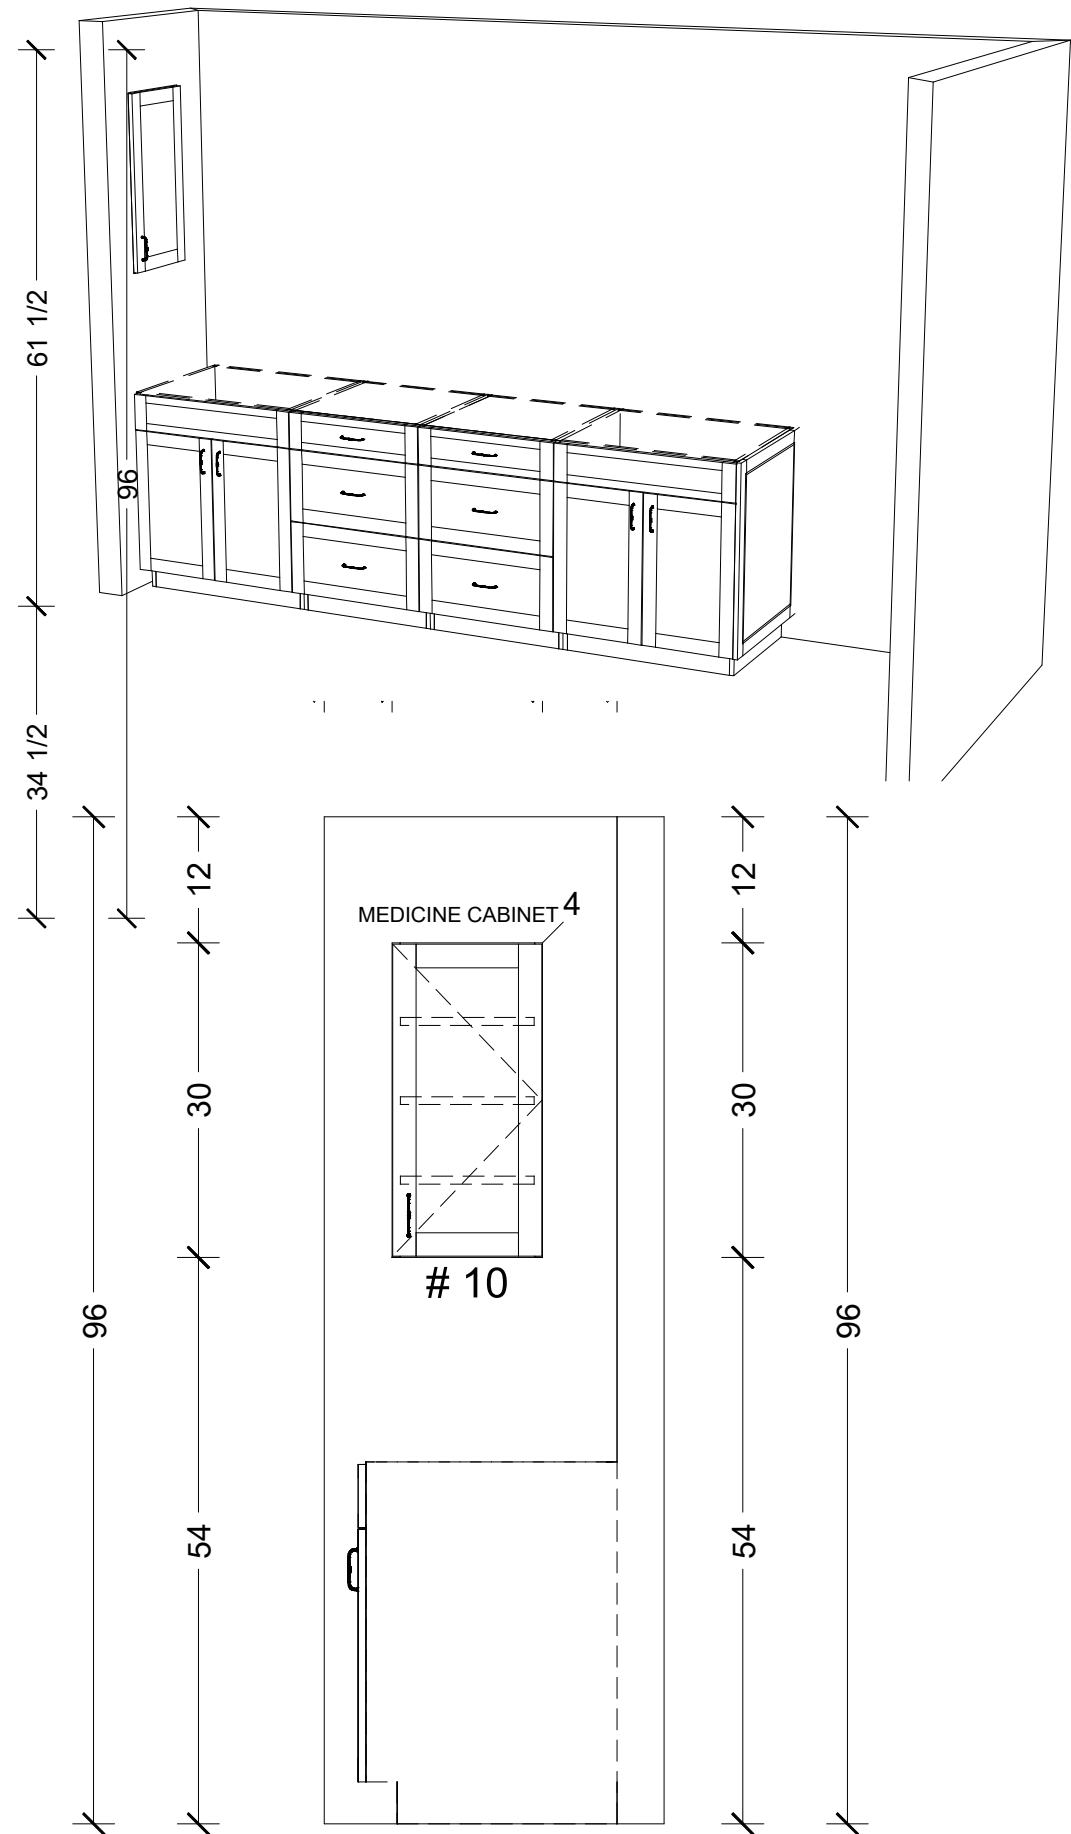



ADVANCED
CABINETS

250 W Anton Ave.
Coeur d' Alene
Idaho 83815
(208) 772-2377

Premier - Lot 4

MASTER BATH

Job #
25243




WO #
0000

Project MGR

Engineer

Date
12/05/25

11 of 19

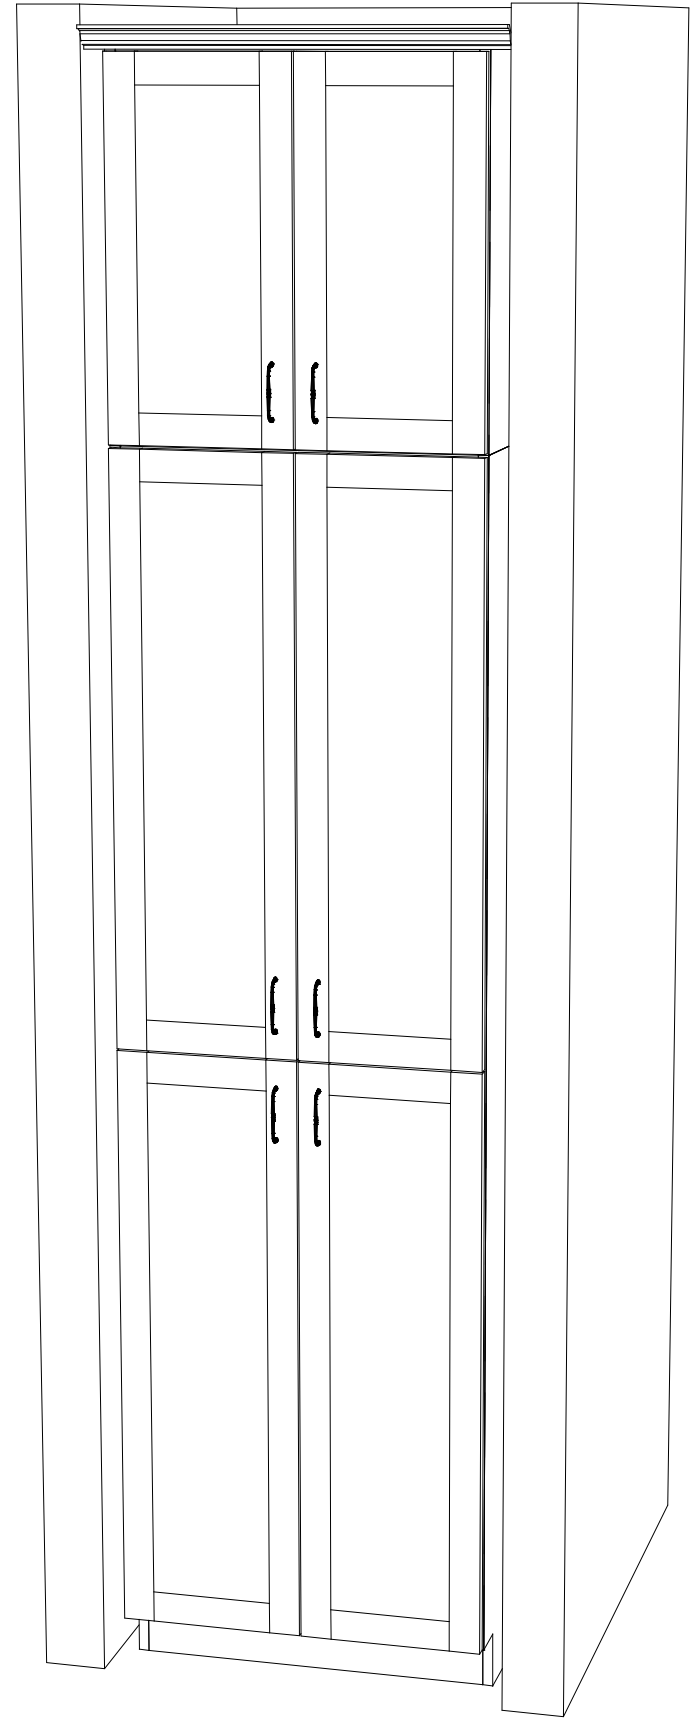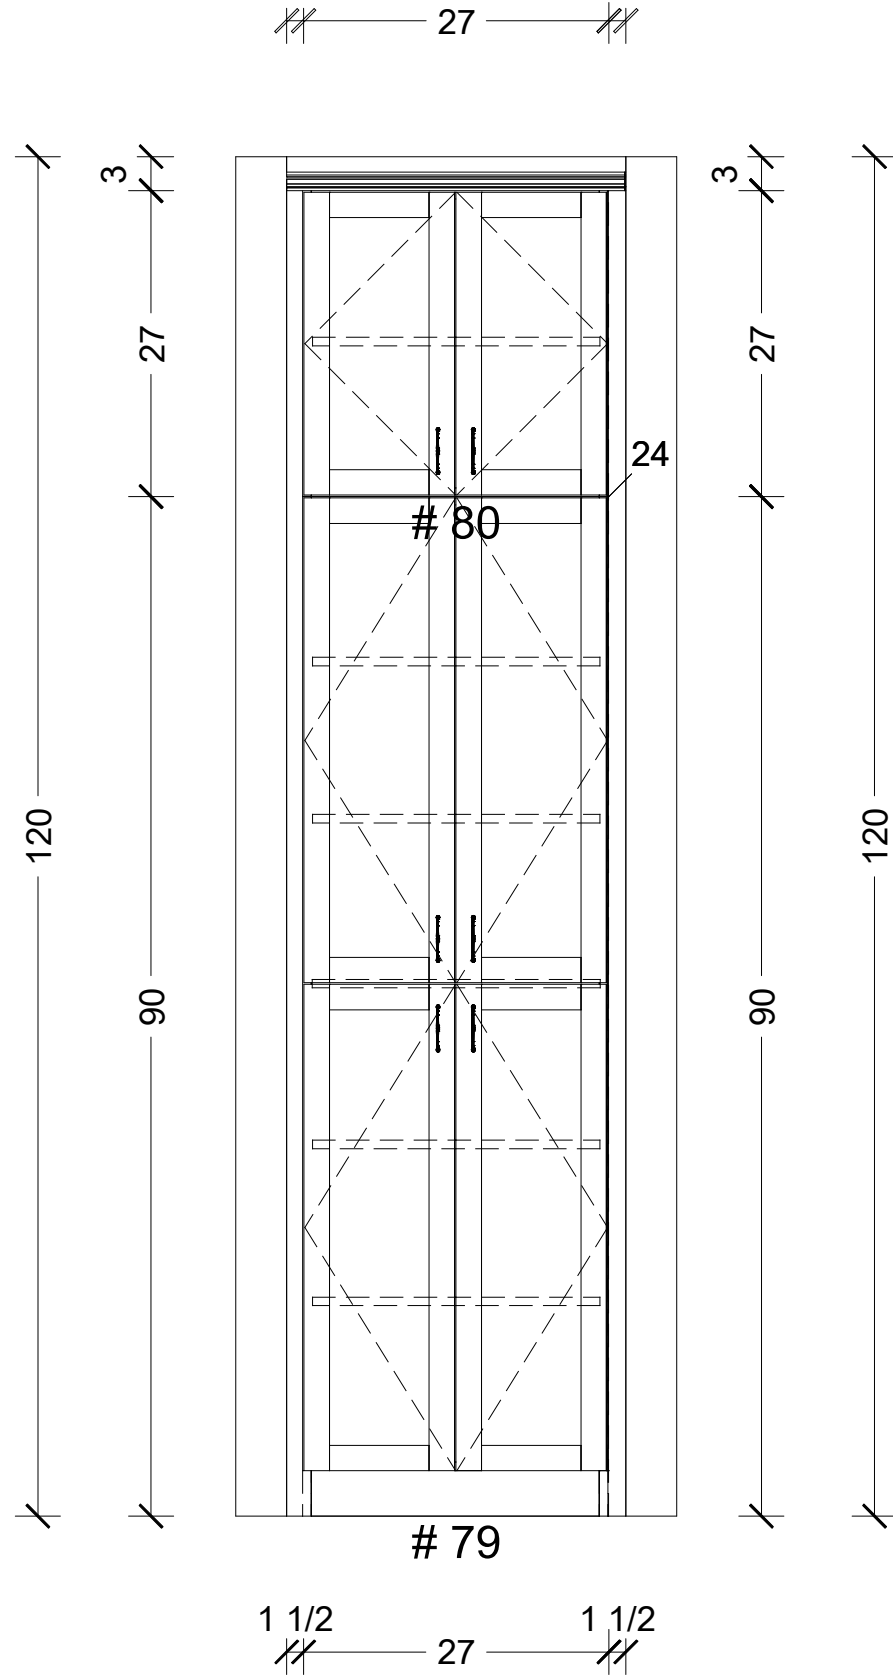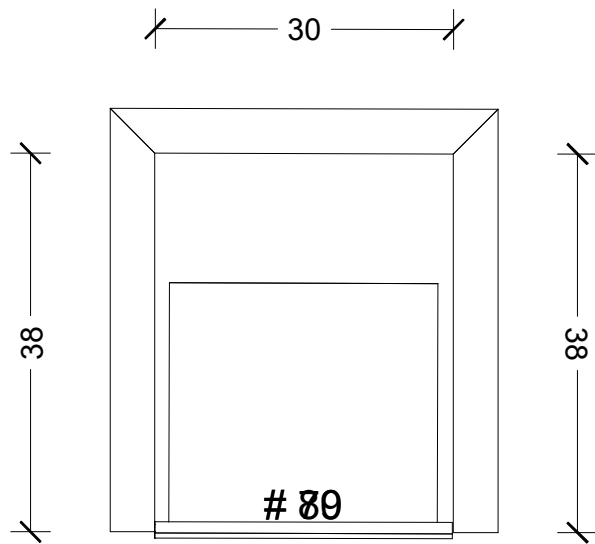

250 W Anton Ave.
Coeur d' Alene
Idaho 83815
(208) 772-2377

ADVANCED
CABINETS



Premier - Lot 4

MASTER BATH LINEN

Job #
25243


WO #
0000

Project MGR


Engineer

Date
12/05/25

12 of 19

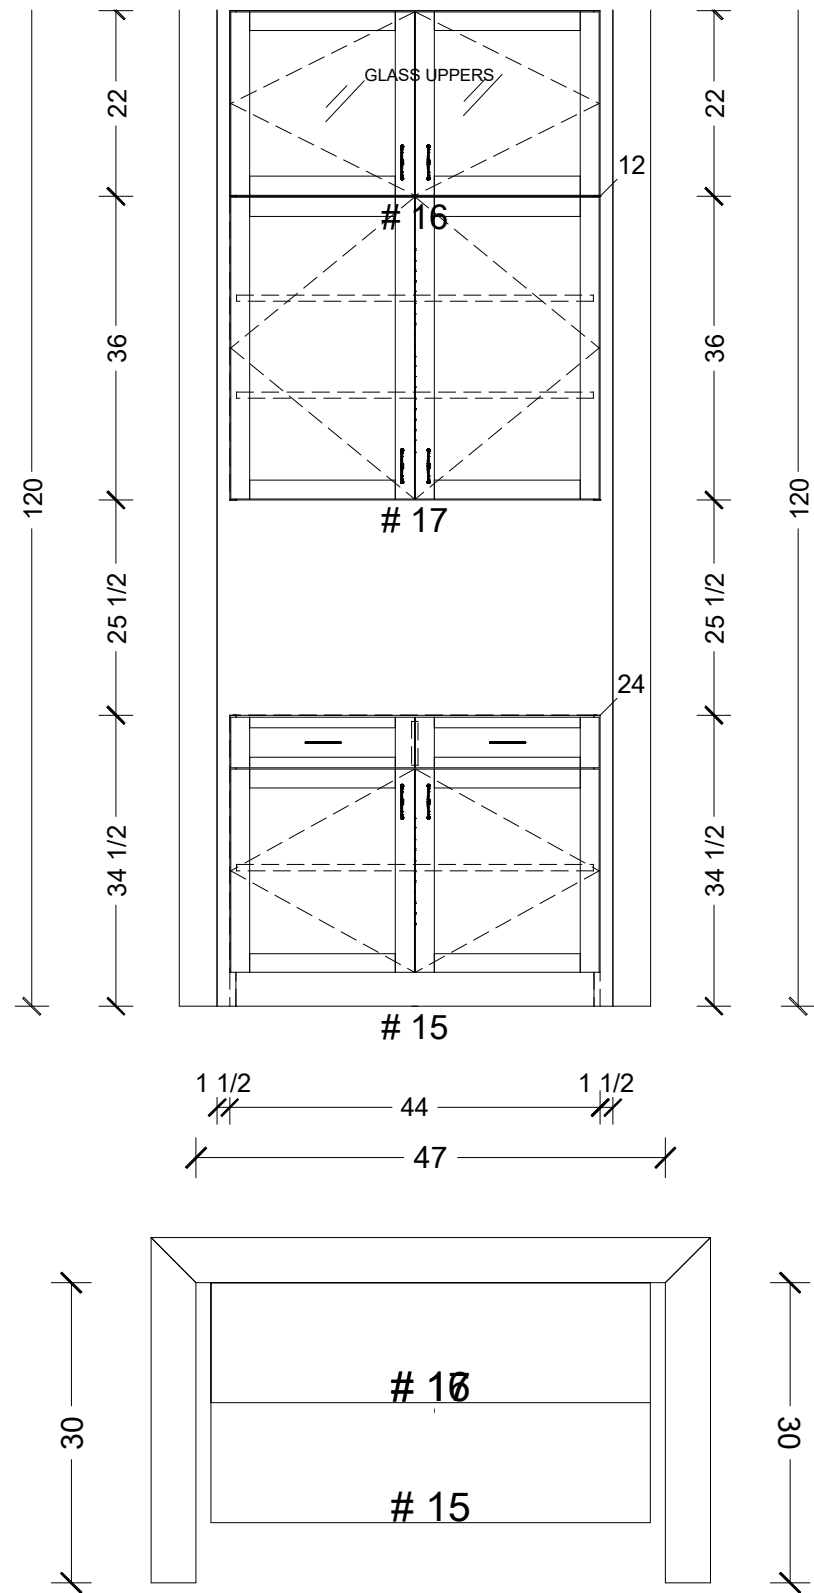

STN-1 STAINED KNOTTY ALDER

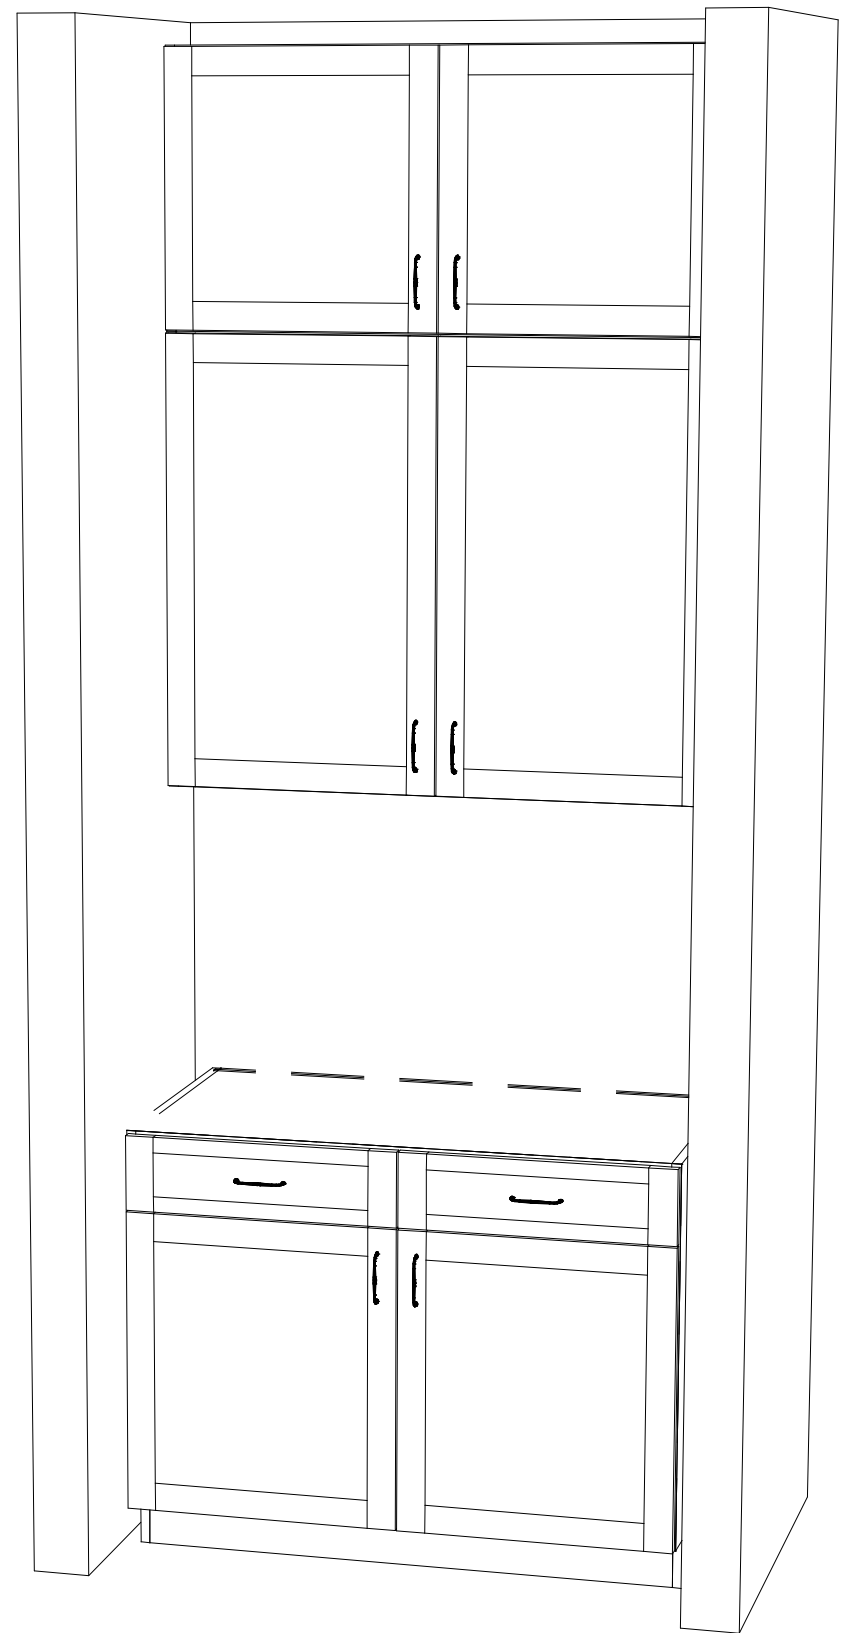

250 W Anton Ave.
Coeur d' Alene
Idaho 83815
(208) 772-2377








Premier - Lot 4
DESK


Job #
25243
WO #
0000
Project MGR

Engineer


Date
12/05/25

13 of 19

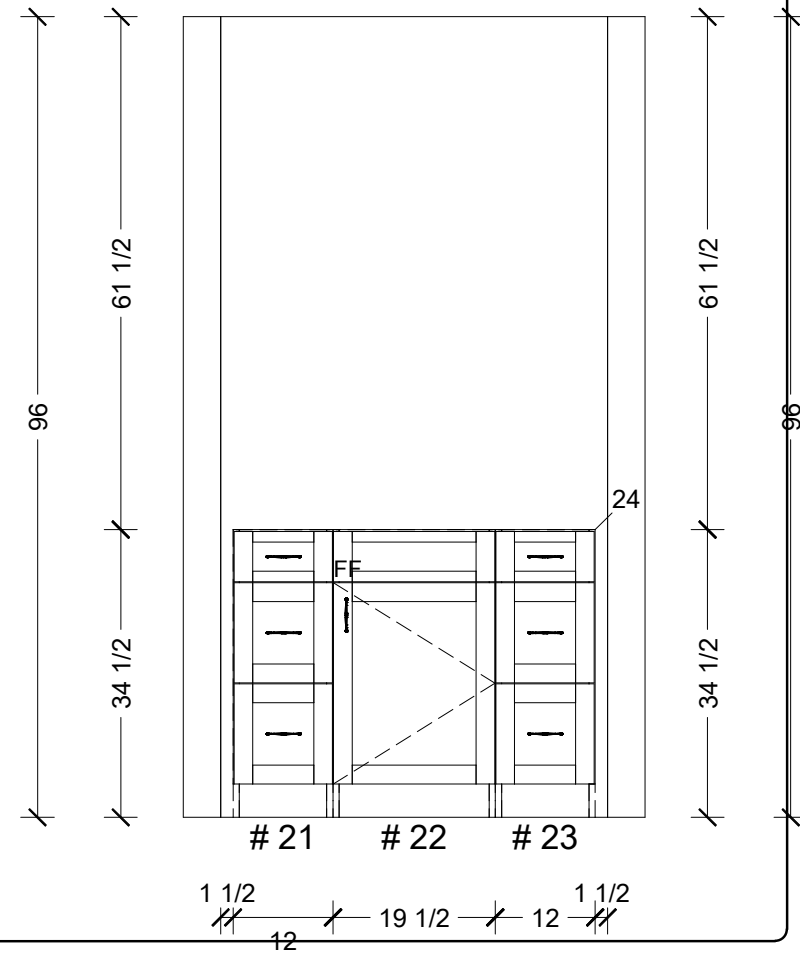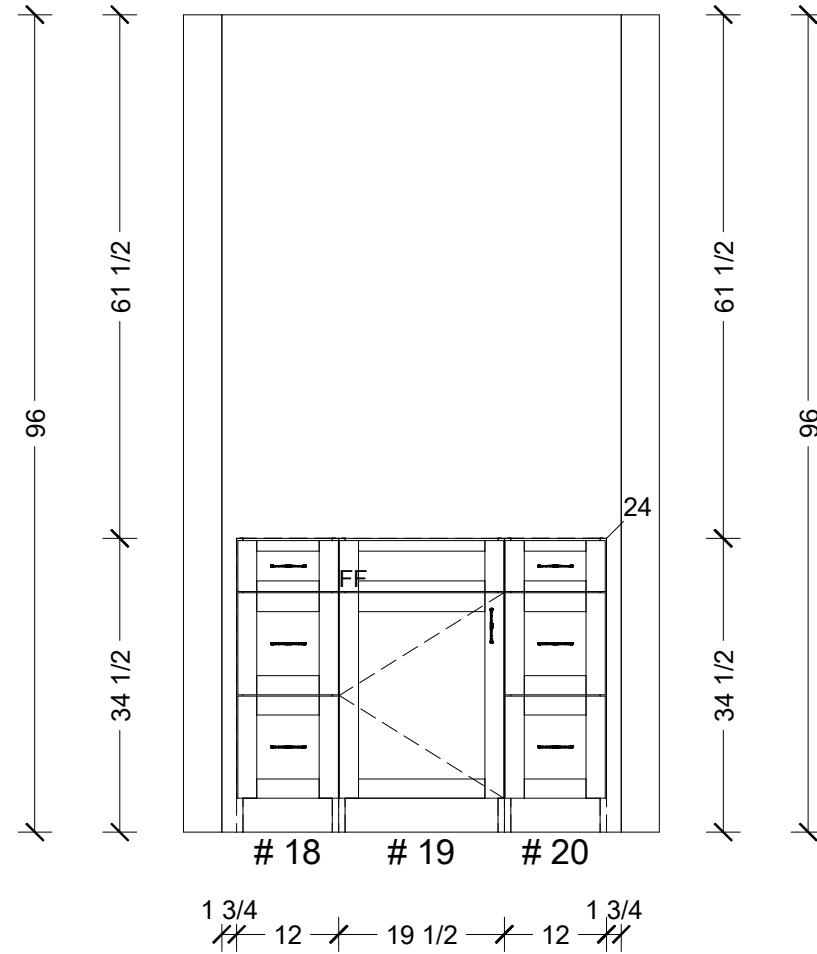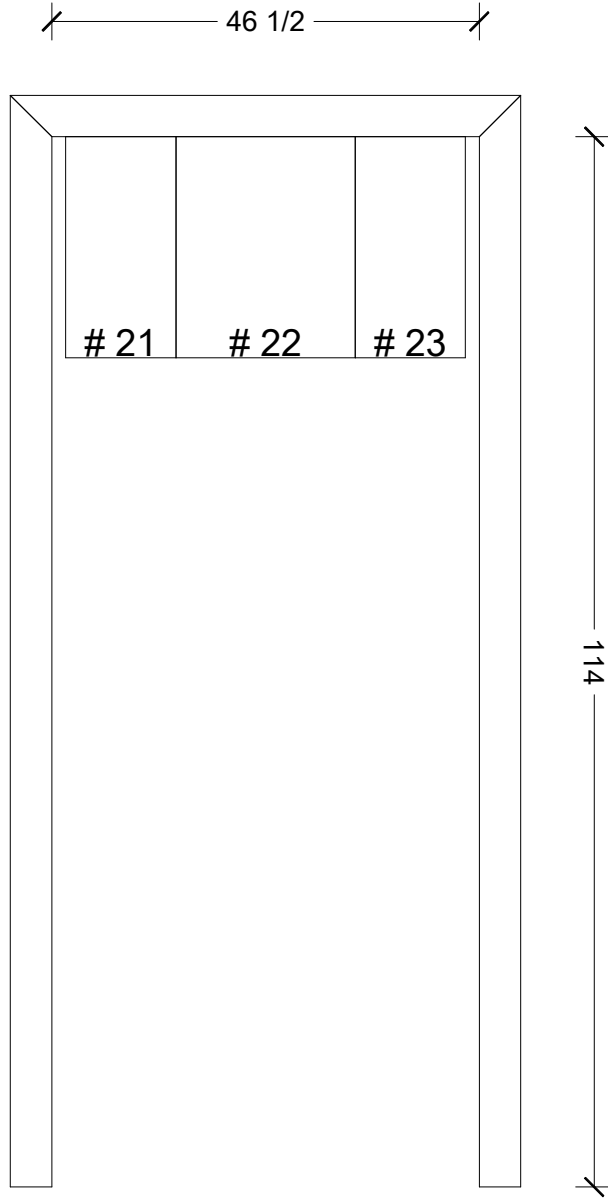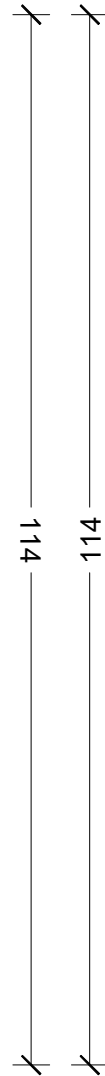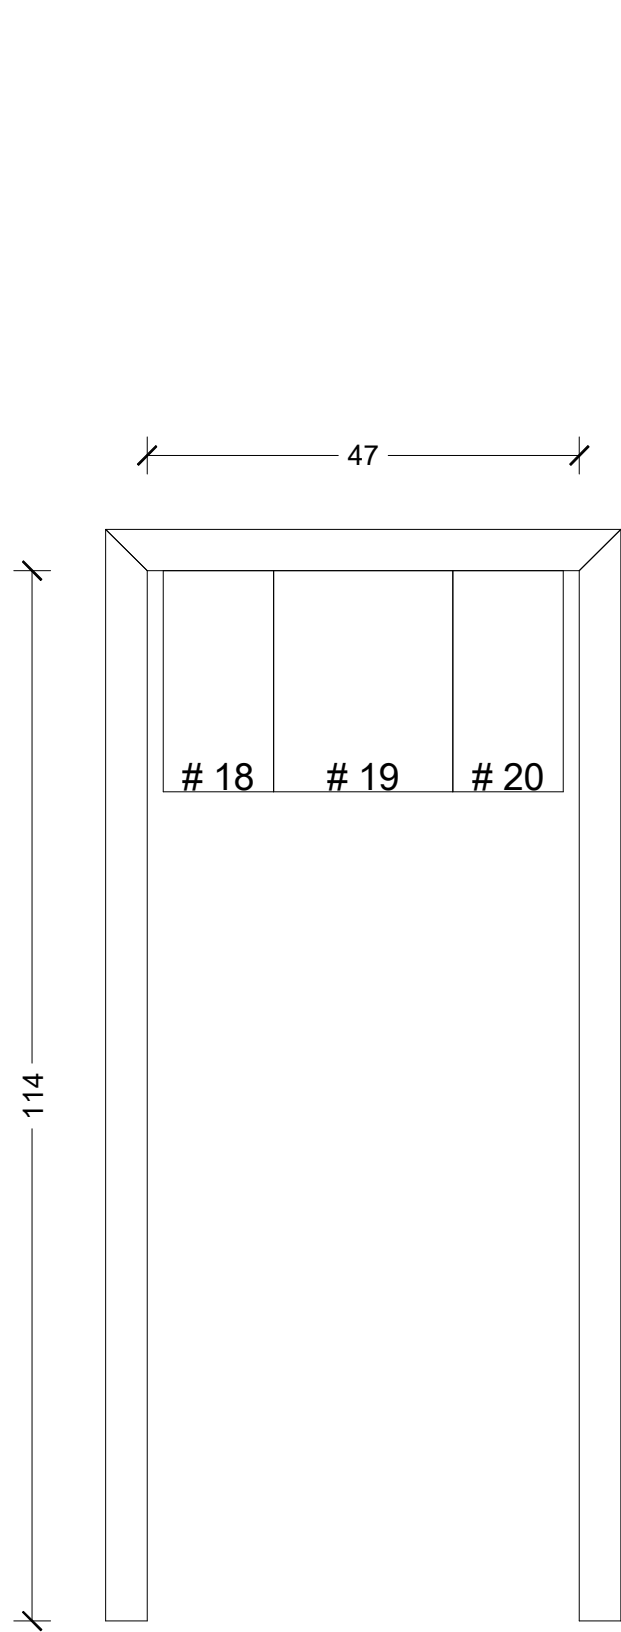

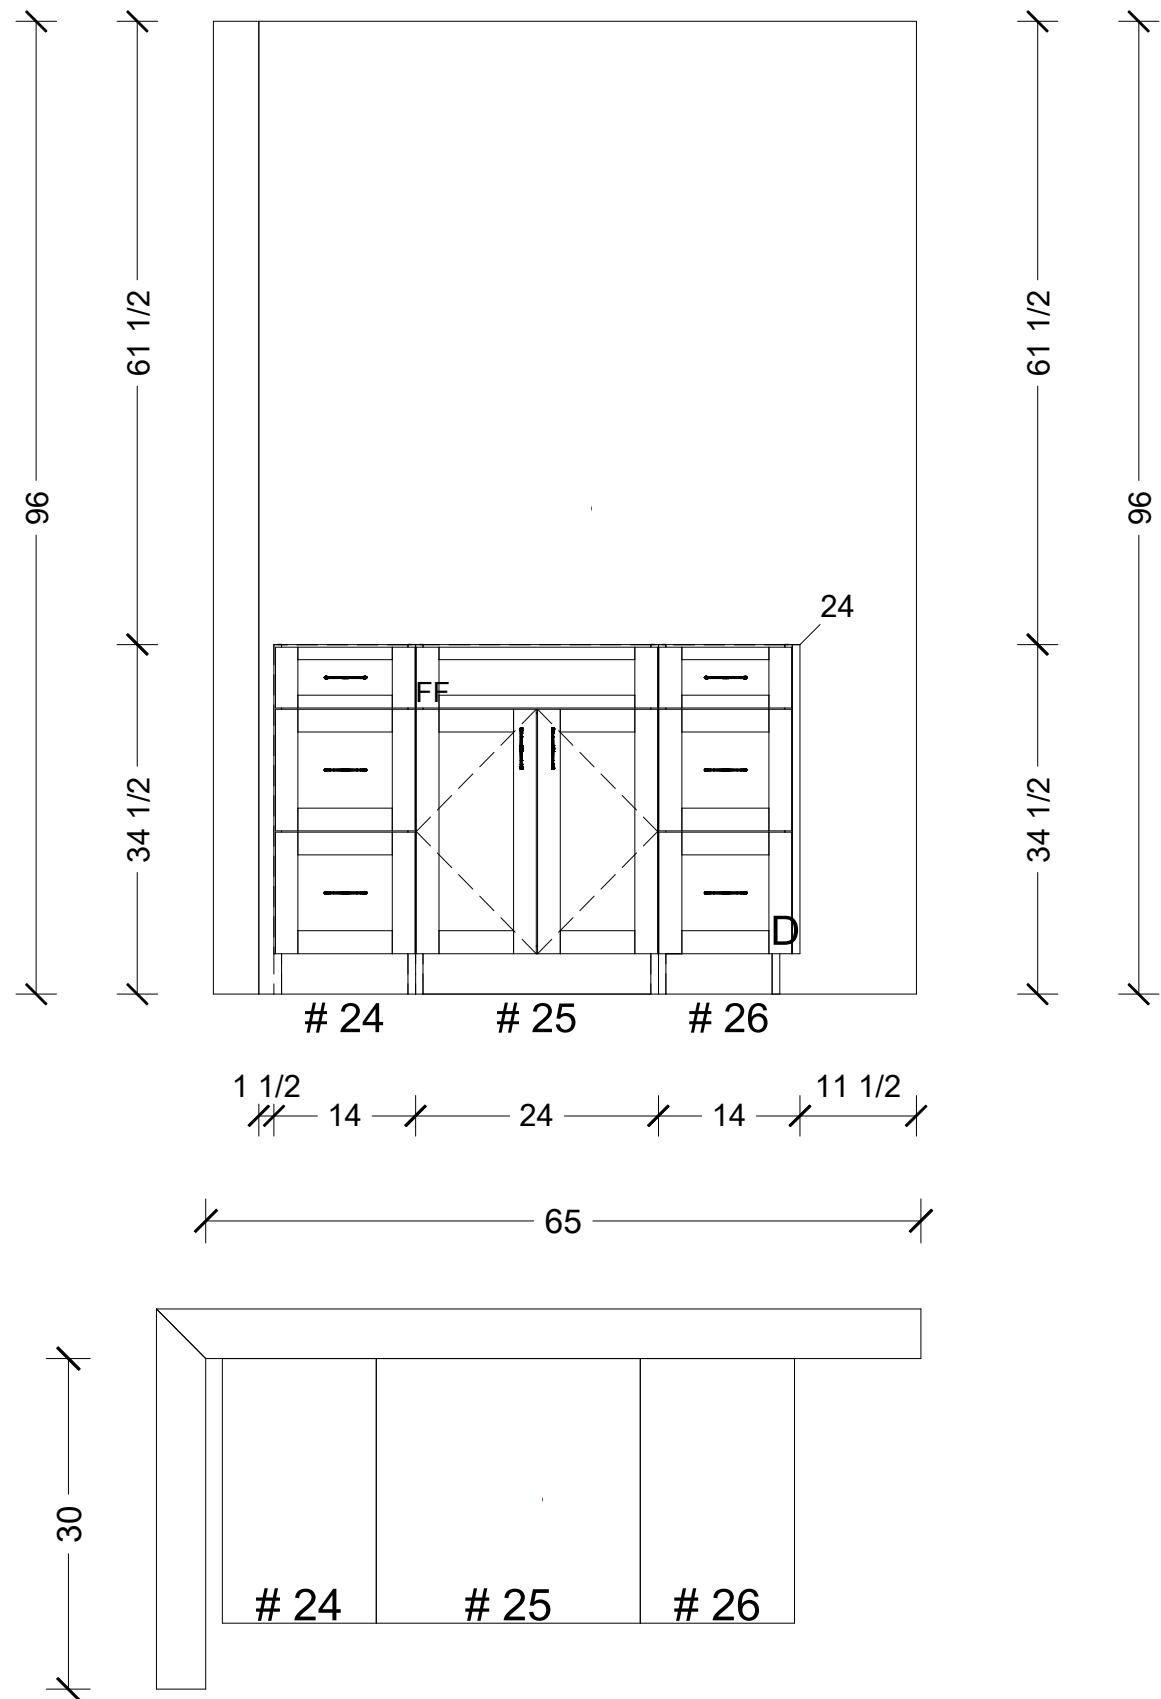

STN-1 STAINED KNOTTY ALDER

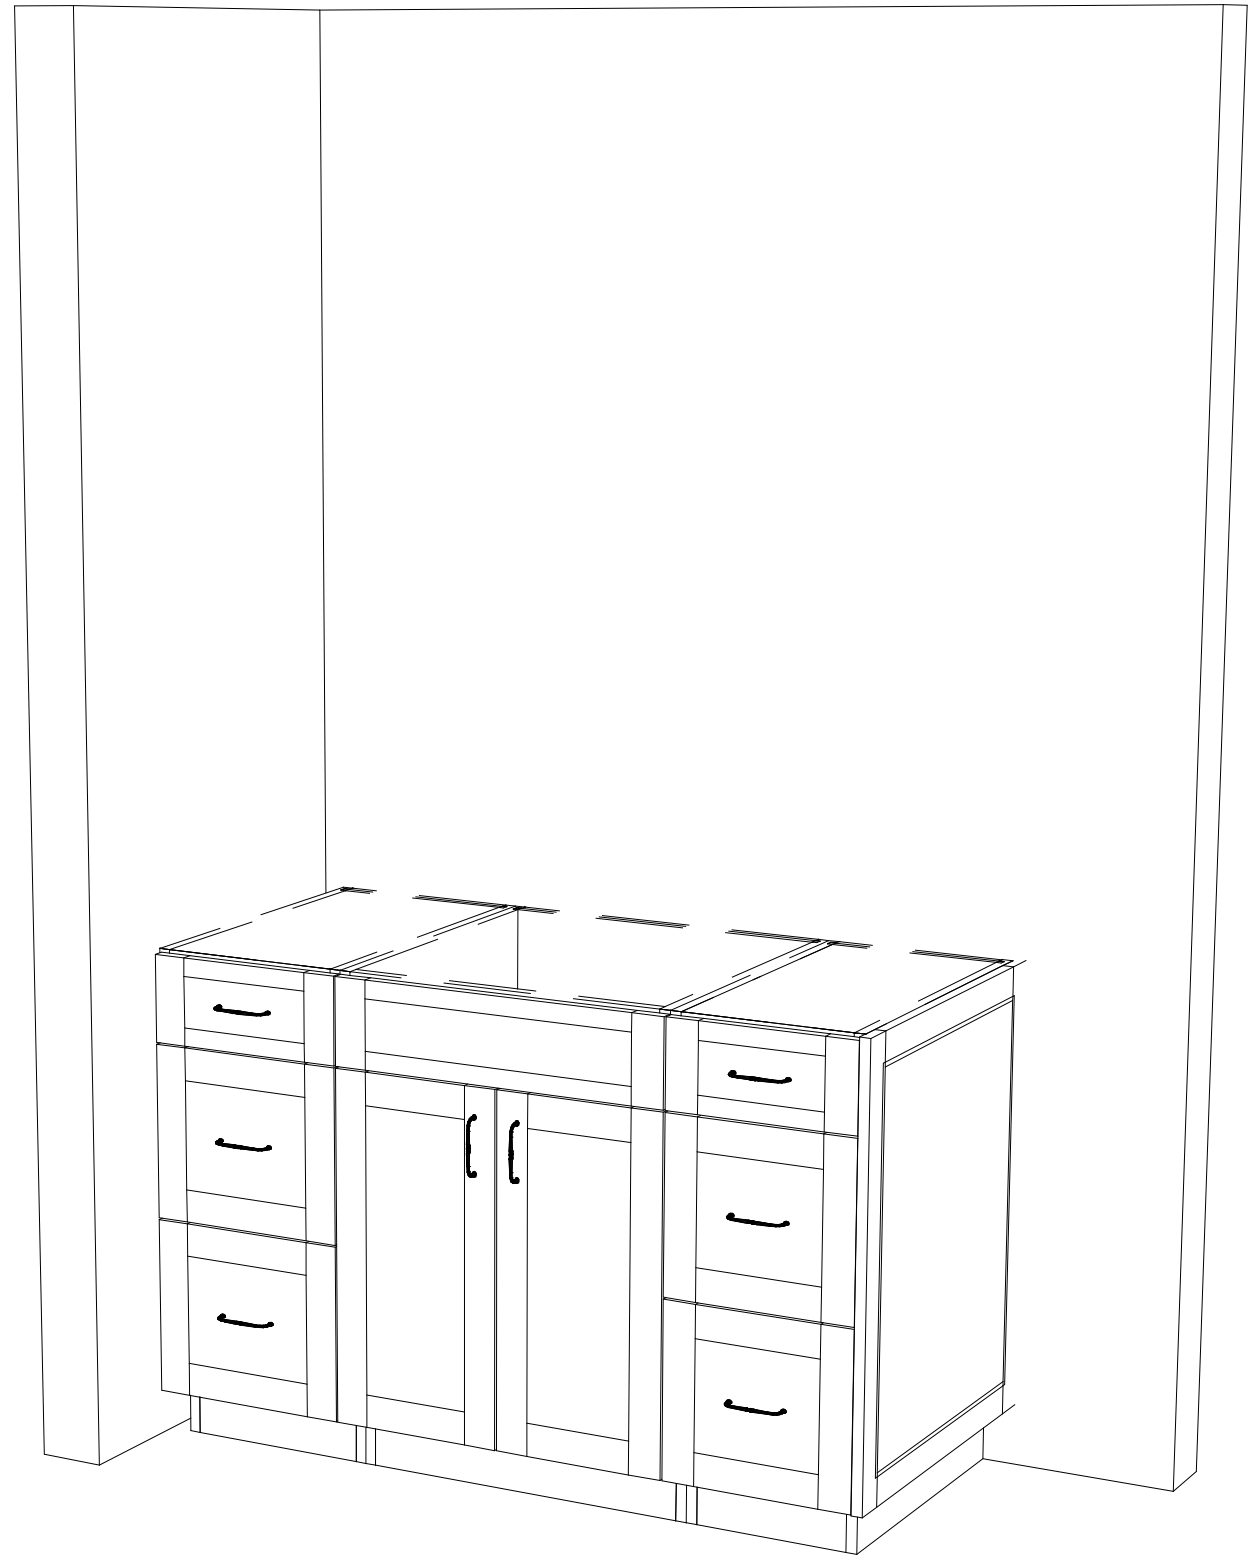

250 W Anton Ave.
Coeur d' Alene
Idaho 83815
(208) 772-2377



Premier - Lot 4

UPSTAIRS BATH

Job #
25243



WO #
0000

Project MGR


Engineer

Date
12/05/25



15 of 19

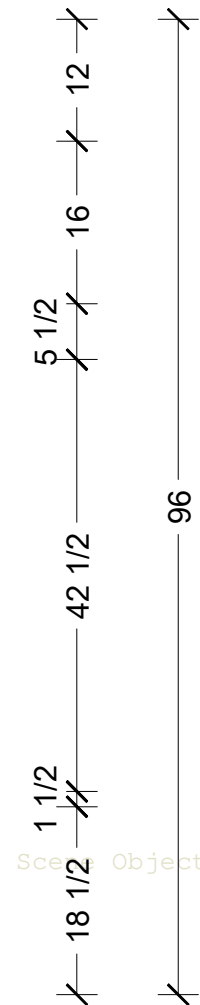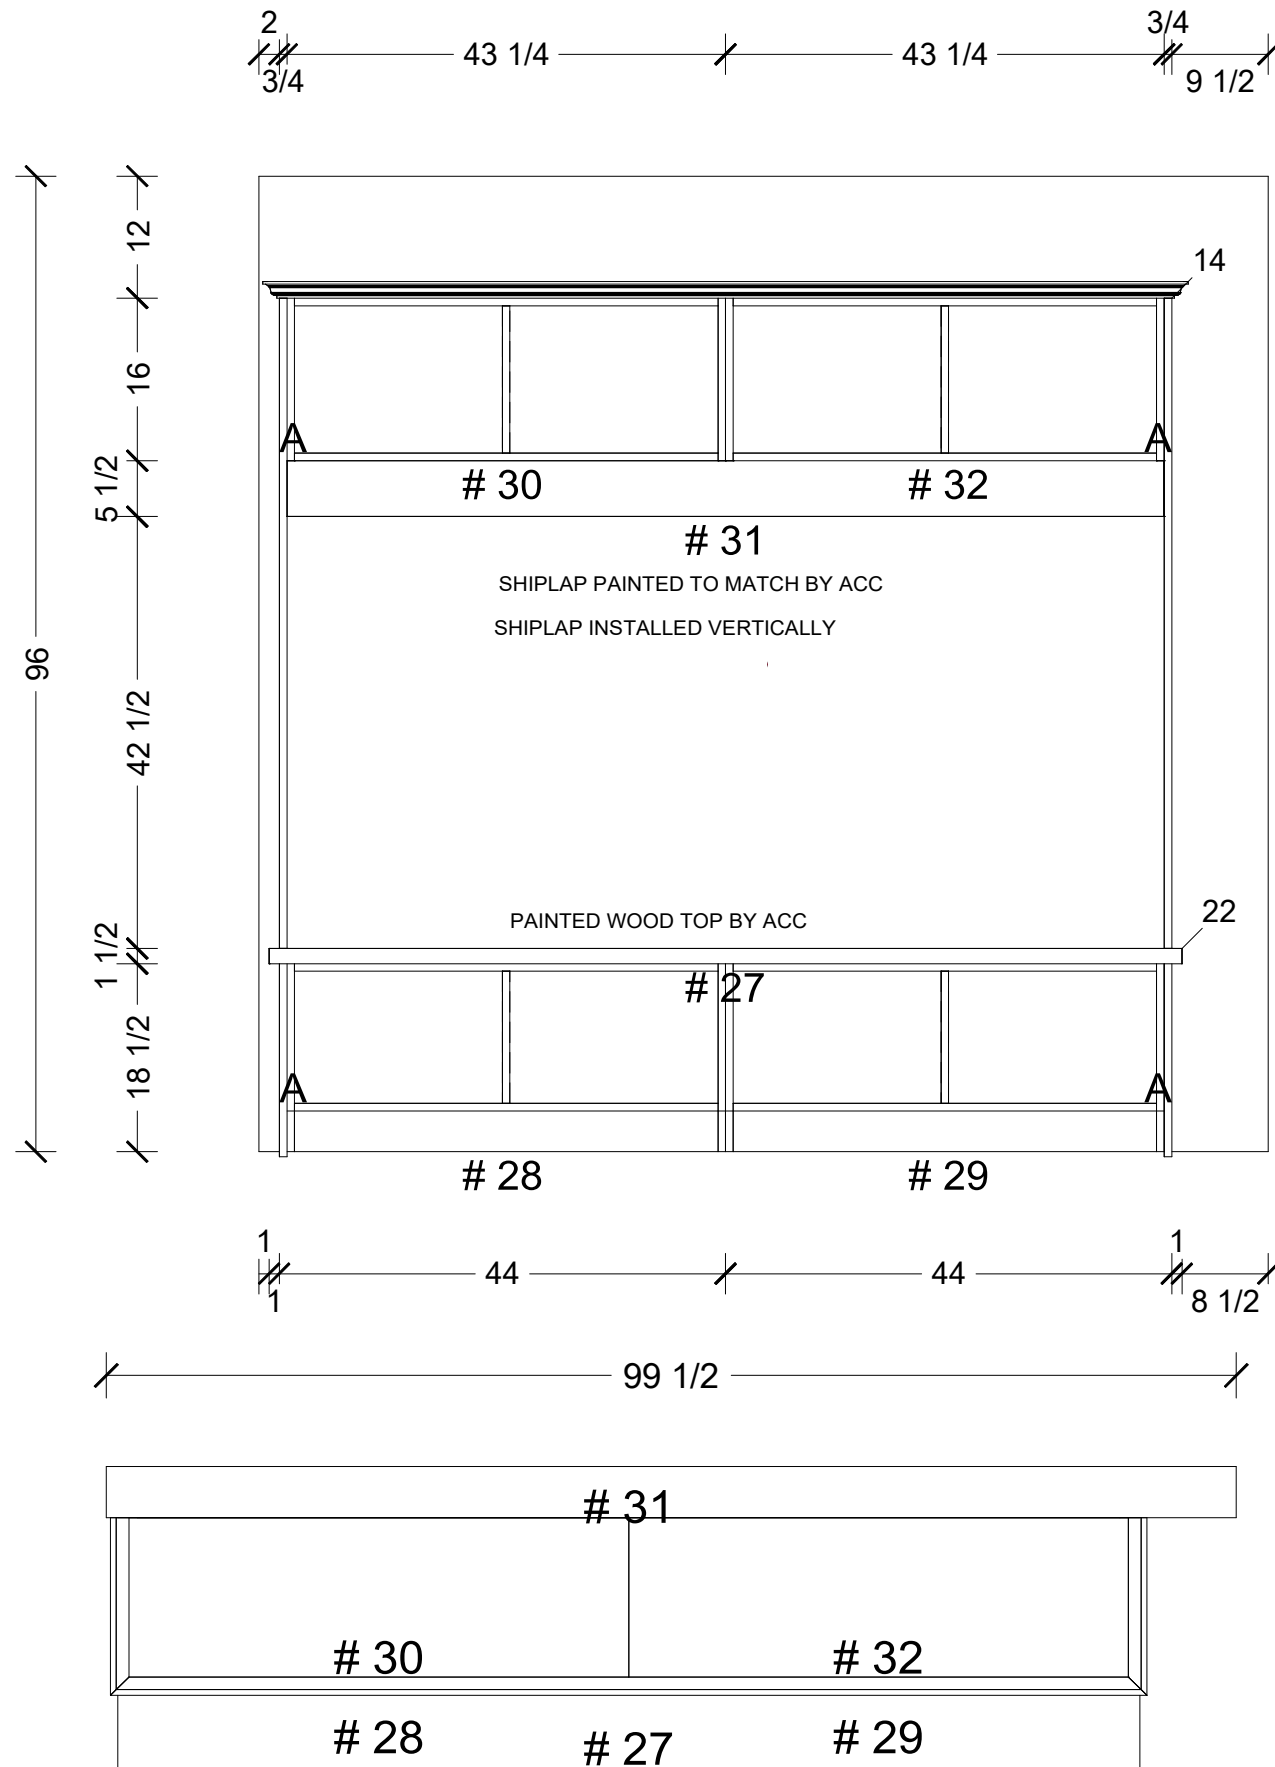

See Object Not Found!

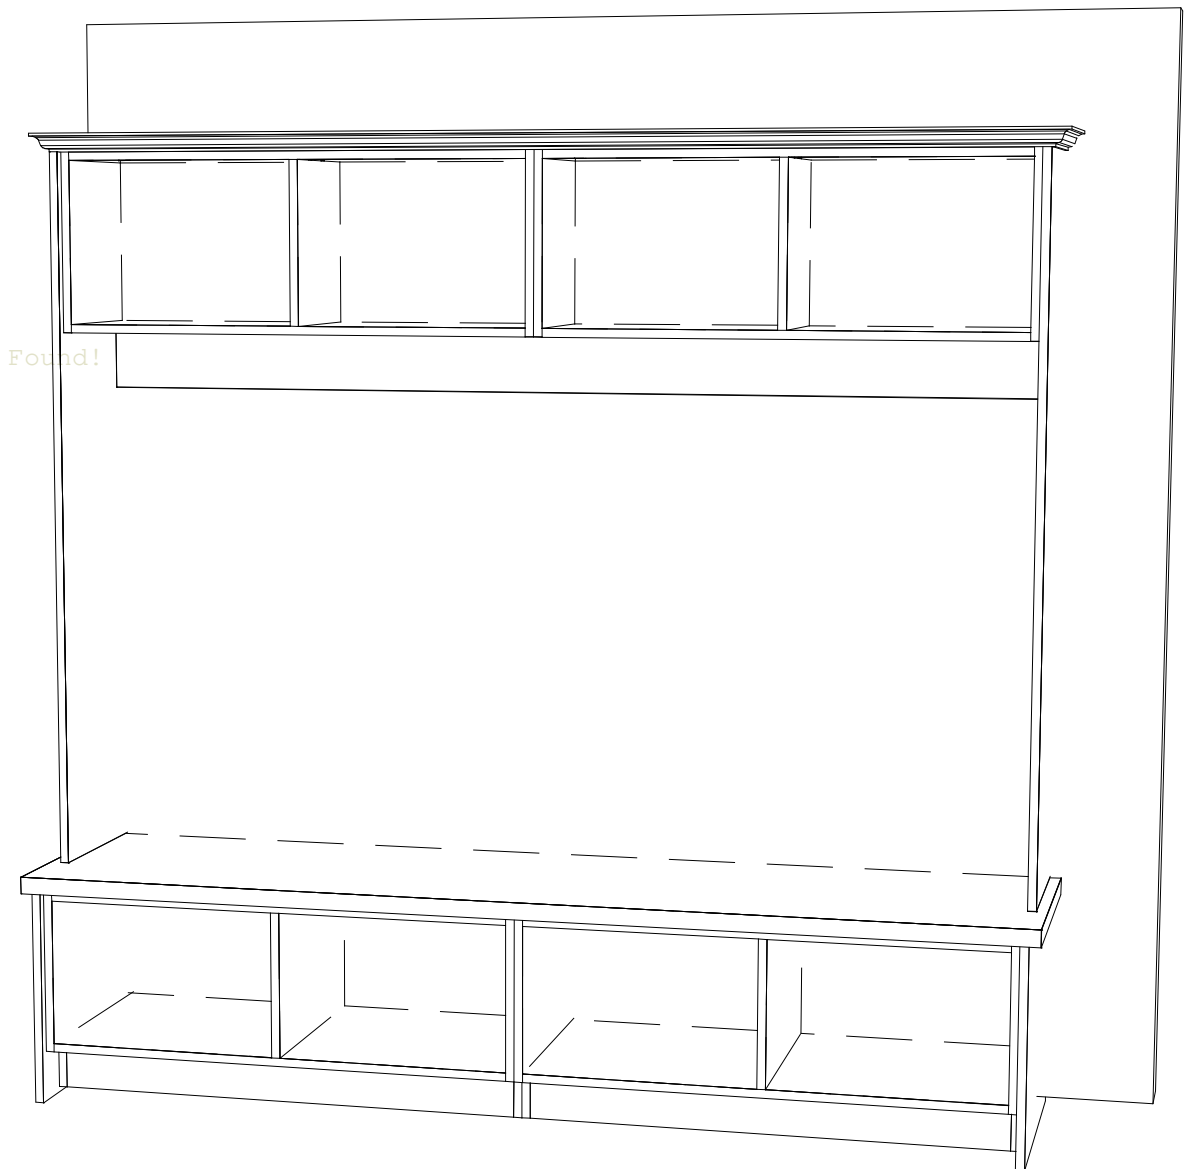

PNT-1 PAINTED SW SAGE 2860

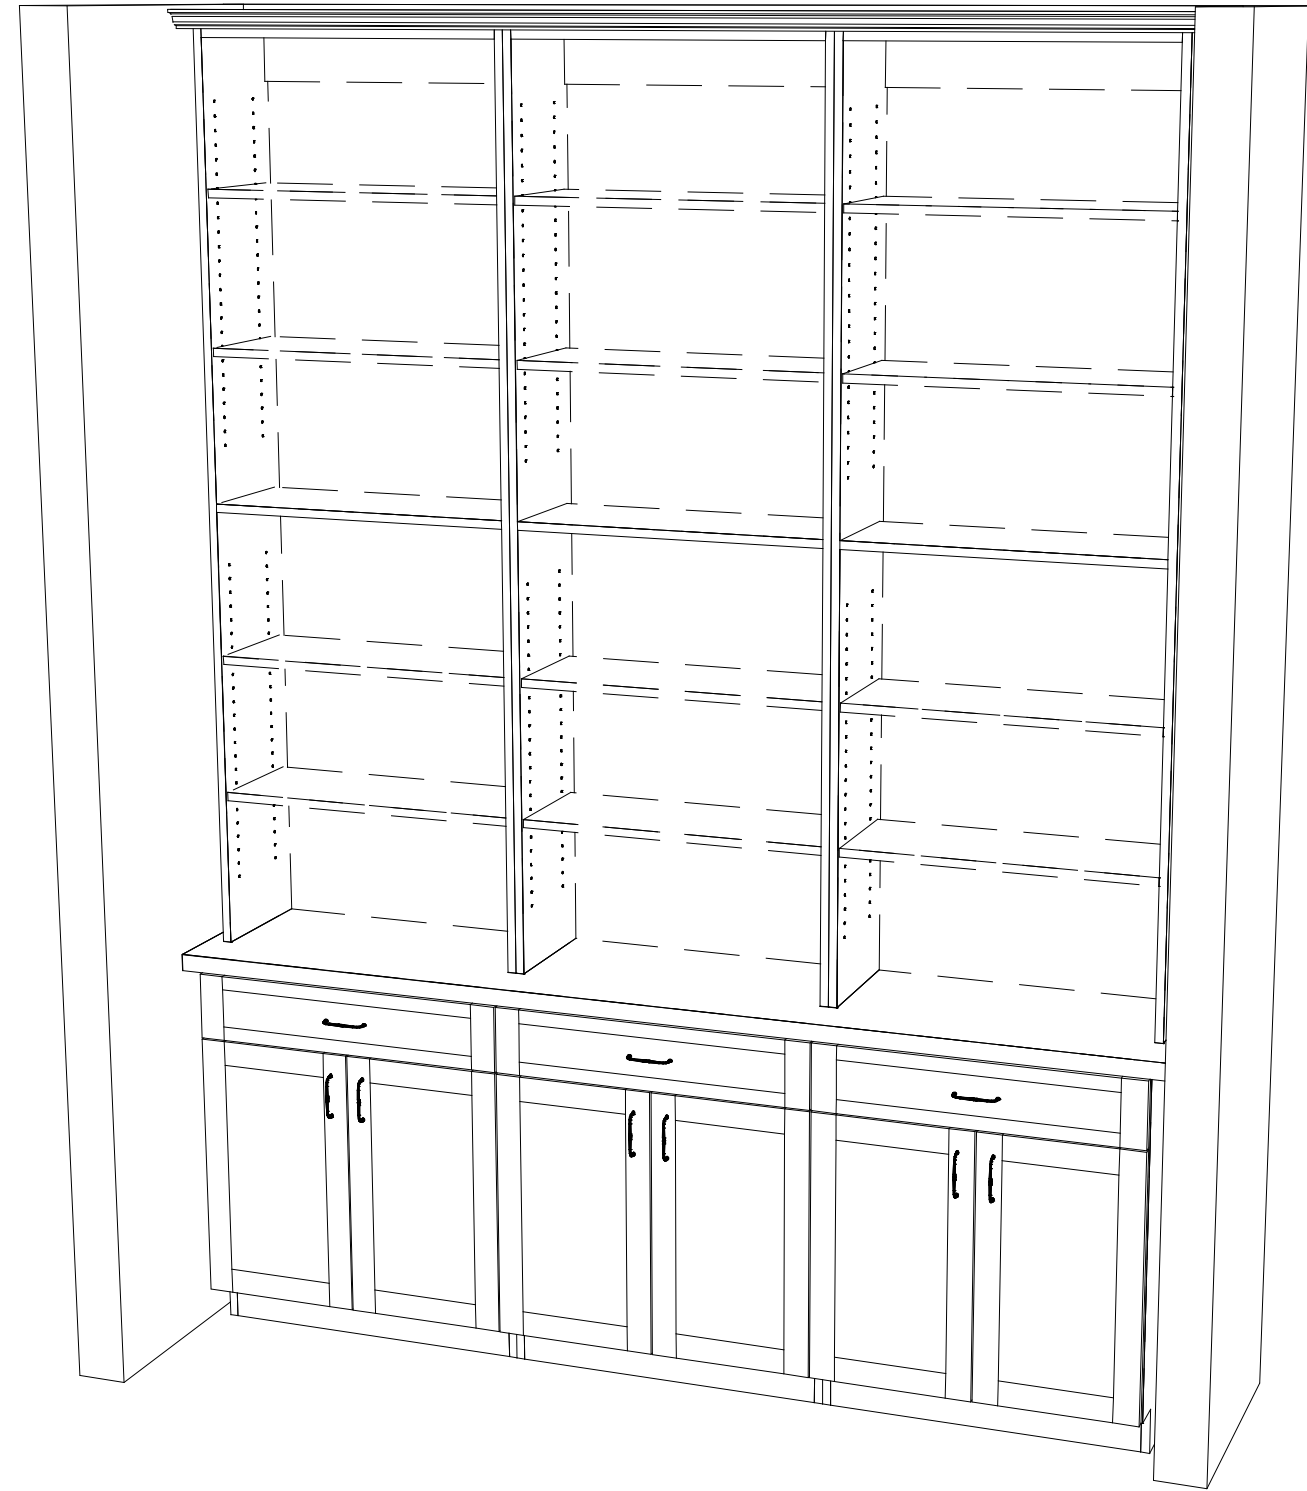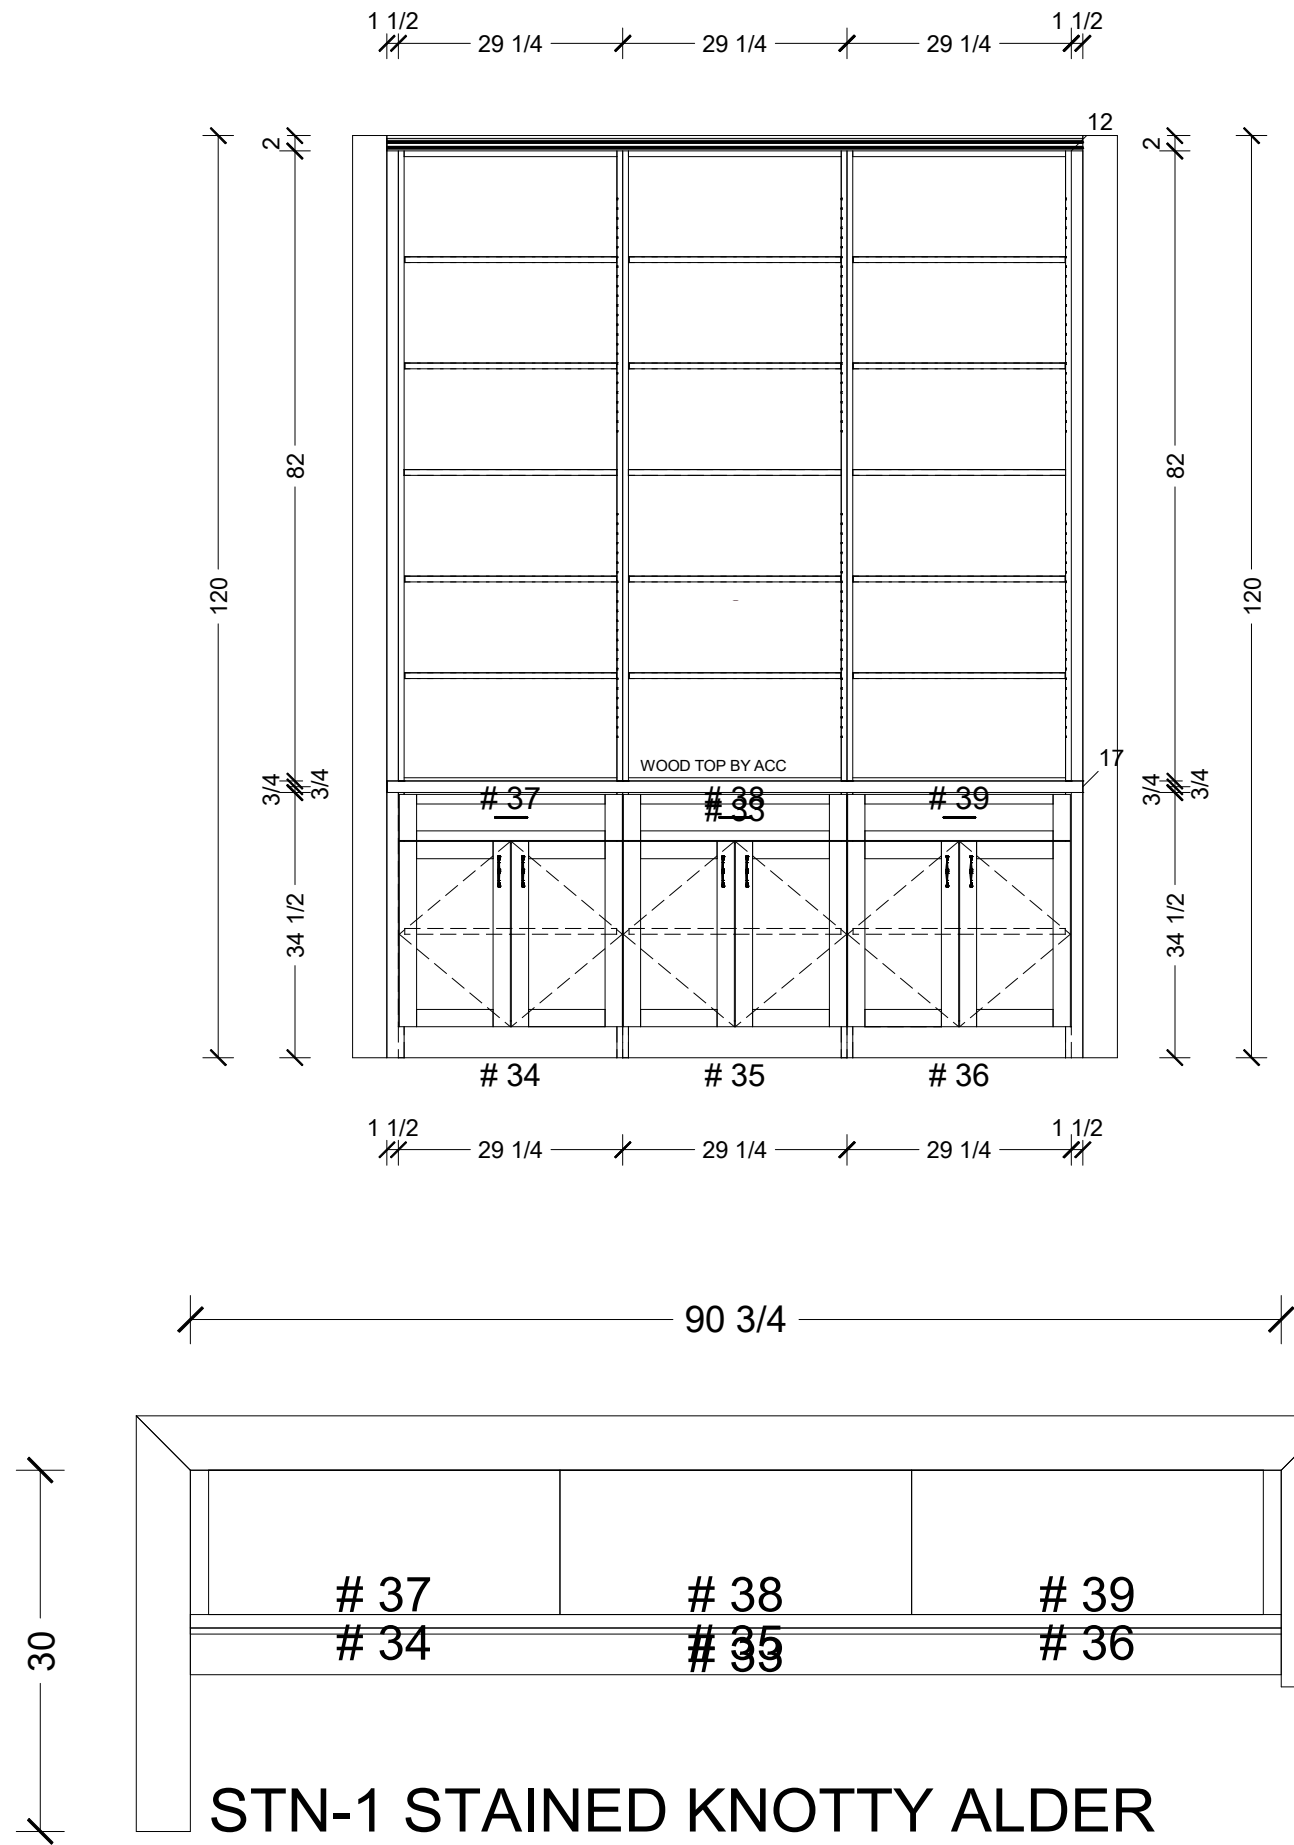

250 W Anton Ave.
Coeur d' Alene
Idaho 83815
(208) 772-2377

ADVANCED
CABINETS



Premier - Lot 4

LIVING OPEN SHELVES

Job #
25243



WO #
0000

Project MGR

Engineer

Date
12/05/25

17 of 19

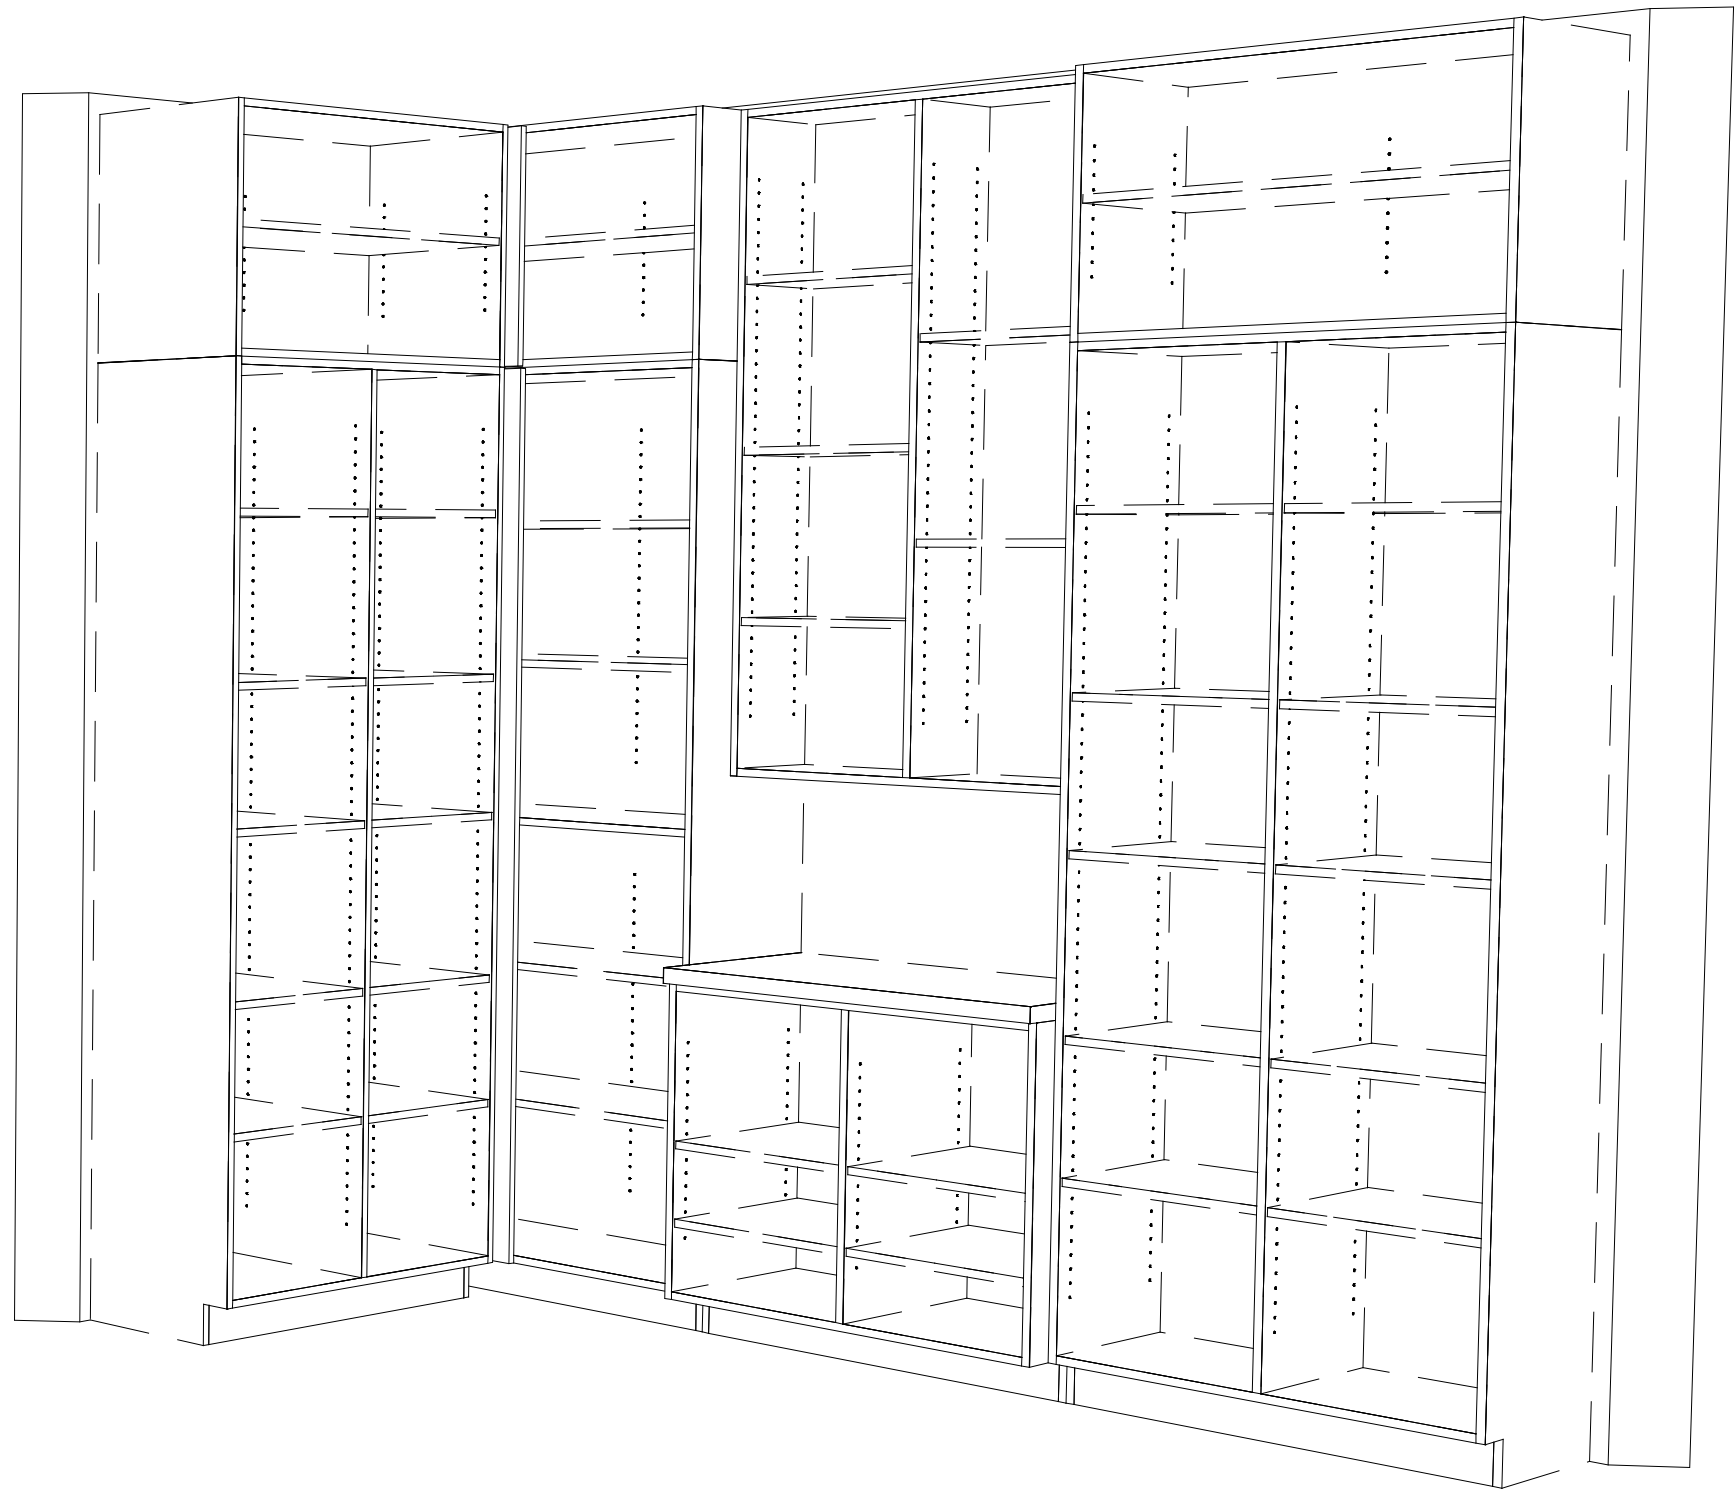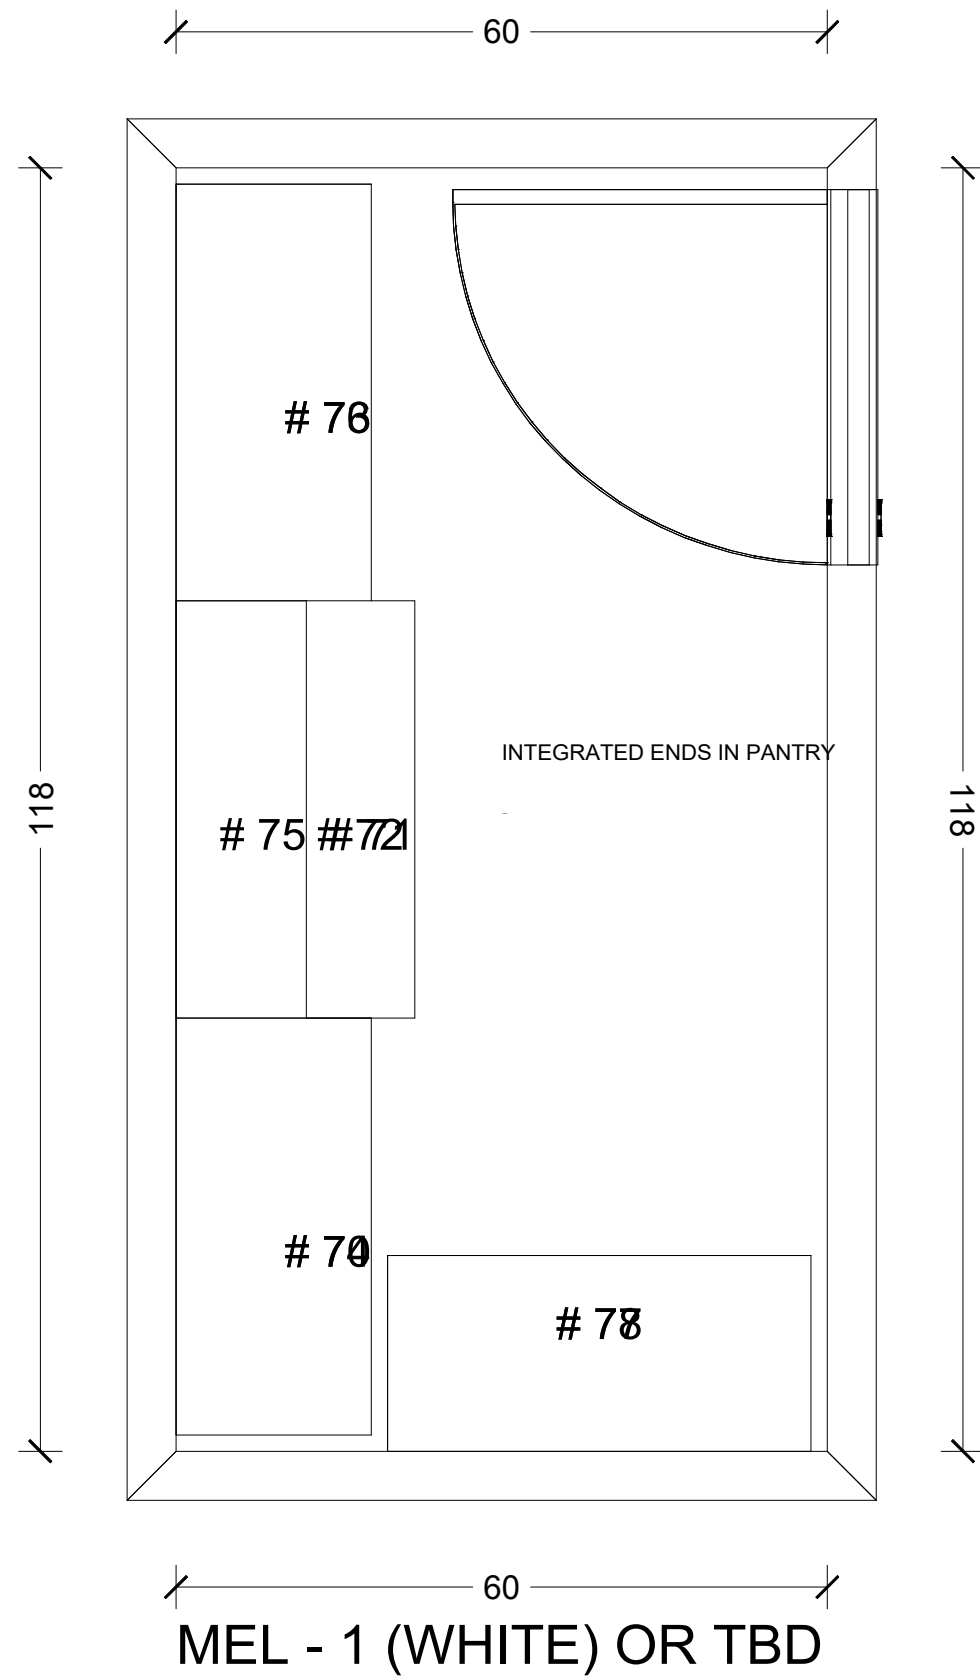

250 W Anton Ave.
Coeur d' Alene
Idaho 83815
(208) 772-2377



Premier - Lot 4

PANTRY TALLS 3D/PLAN

Job #
25243

WO #
0000

Project MGR

Engineer

Date
12/05/25

18 of 19

